① 基地硬條件與環境

基地　40 M × 55 M ≈ 2,200 ㎡（題目給定），略平坦（高差約 0.5 M）
分區　住宅區　建蔽 40%／容積 120%（低容積）
臨路　20 M 道路
四鄰　東側國民小學；附近傳統市場（步行可及）
基地內　老樹兩株（題目給定）
氣候　夏西南風／冬東北風
水文　舊社區排水老舊、暴雨有淹水紀錄
△ 低容積（120%）是本題的機會：可低層化，把地讓給戶外與綠地。
⚠ 老樹依各地《樹木保護自治條例》檢討，原地保留為本案選擇。



② 英雄條件・課題與對策

英雄條件：基地內老樹兩株

課題 1　微氣候（呼應申論）：熱島、通風不良、缺綠
對策　留西南—東北通風廊道貫穿；增綠覆與遮蔭；
淺色高反射鋪面；水緣（雨花園）降溫
課題 2　老樹兩株易被量體與施工犧牲
對策　建築退讓、不造樹冠投影；樹下設室外家具為戶外核心
課題 3　舊社區排水老舊、暴雨淹水
對策　地面層抬高 +0.5 M、透水鋪面、雨花園滯蓄後放流
本案不設地下室（D＝0），從源頭避開淹水風險
課題 4　高齡使用者的安全與便利
對策　單層化動線、近電梯、平緩坡道、防滑、近保健室
課題 5　東側國小接送尖峰與樂齡接送衝突
對策　樂齡接送彎設 20 M 道路側，並與國小尖峰時段錯開




縮圖示意・不代表比例；正圖見中欄配置。

③ 空間需求・量體與開放空間

法規檢核（A/B/G/F/D 五帳）


項目	法定	本案	
基地 A	—	**2,200 ㎡**	—
建蔽率	40%	**29.5%**	✓
建築面積 B	≤880 ㎡	**648 ㎡**	✓
容積率	120%	**58.9%**	✓
計容積 F	≤2,640 ㎡	**1,296 ㎡**	✓
開挖率 D/A	未給上限	**0%（不設地下室）**	—

主棟（教室・活動・共餐）480 ㎡ × 2F ＝ 960 ㎡
保健・行政・諮詢 168 ㎡ × 2F ＝ 336 ㎡
⚠ 空間項目面積題目未逐項給定 → 全部標為自訂方案。
戶外：老樹客廳約 600 ㎡、雨花園約 120 ㎡〔方案〕
容積只用 58.9%——低層化換取戶外活動與綠地，正面回應微氣候。

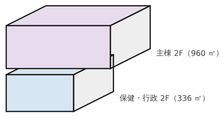


④ 人車動線・防災與管理

人行　主入口設北側 20 M 道路；西側次入口接傳統市場日常人流。
接送　樂齡接送彎在 20 M 道路側，與東側國小尖峰時段錯開。
無障礙　全程平緩坡道、防滑鋪面、近電梯與保健室。
停車　題目未指定車位數 → 圖上明寫未指定；地面設接送與自行車位。
防災　老樹客廳為無建物地震臨時避難集合場。
防洪　地面層抬高 +0.5 M；雨花園滯蓄後放流；不設地下室。
微氣候　通風廊道貫穿、複層綠覆遮蔭、淺色高反射鋪面。
管理　共餐與活動可分時段；保健諮詢可獨立開放。

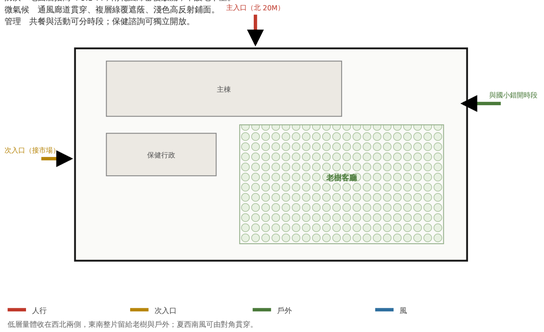

低層量體收在西北角側，東南整片留給老樹與戶外；夏西南風可由對角貫穿。

全區配置與地面層景觀

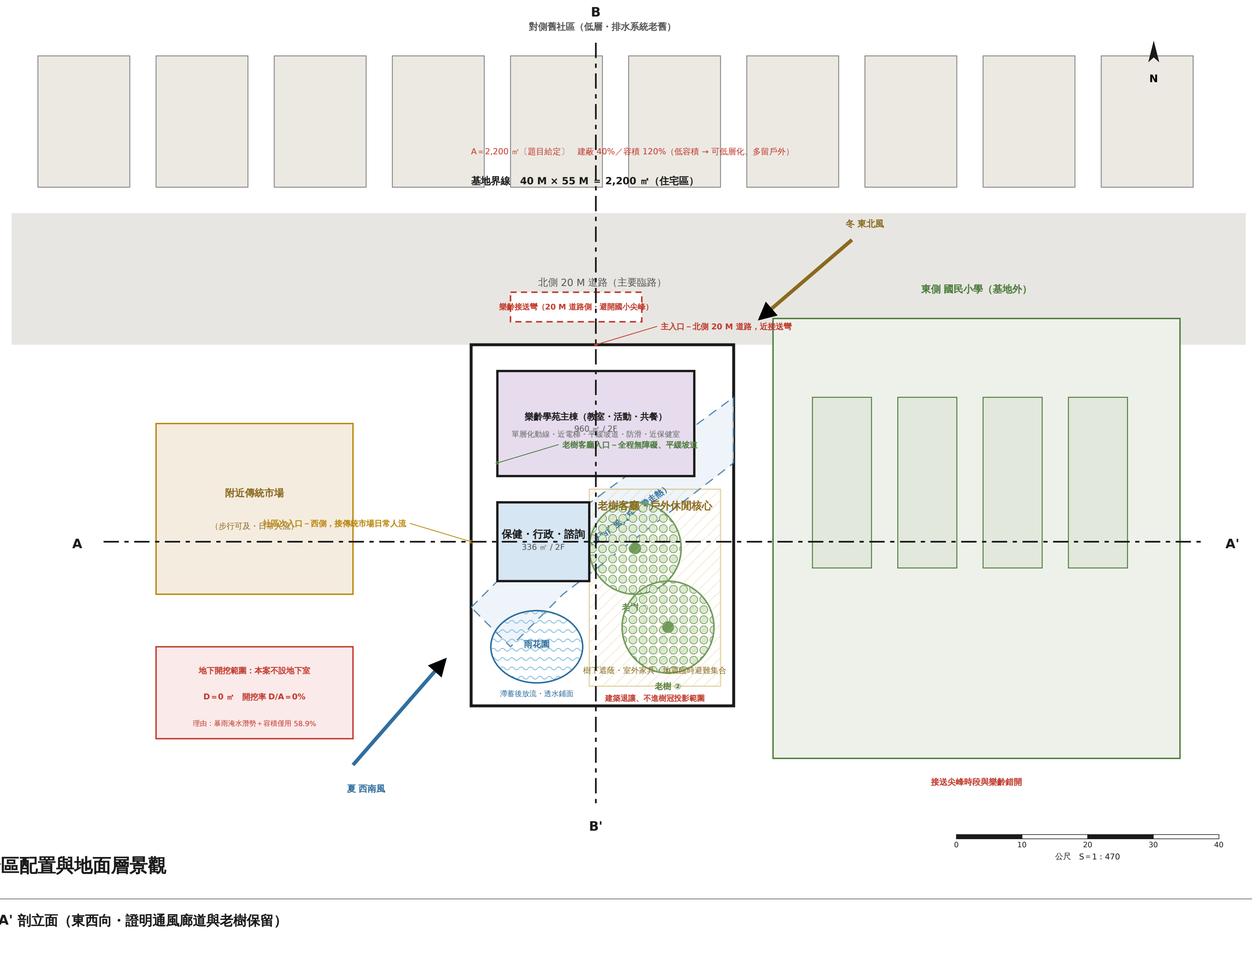


A-A' 剖立面（東西向・證明通風廊道與老樹保留）




1F 4.2 M／2F 3.6 M，地面層抬高 +0.5 M。老樹樹冠高於量體，建築退出樹冠投影，風由西南穿越不被擋。

B-B' 剖立面（南北向・證明低層化與防淹）

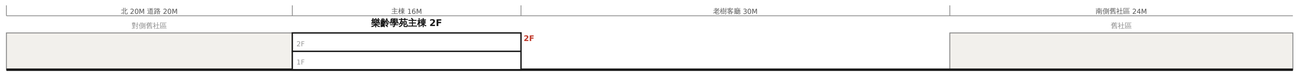

本案僅 2 層，與周邊低矮舊社區同尺度；地面層抬高 +0.5 M 並設防水閘，不設地下室，淹水風險由源頭消除。

局部透視　老樹客廳（午後活動時段）

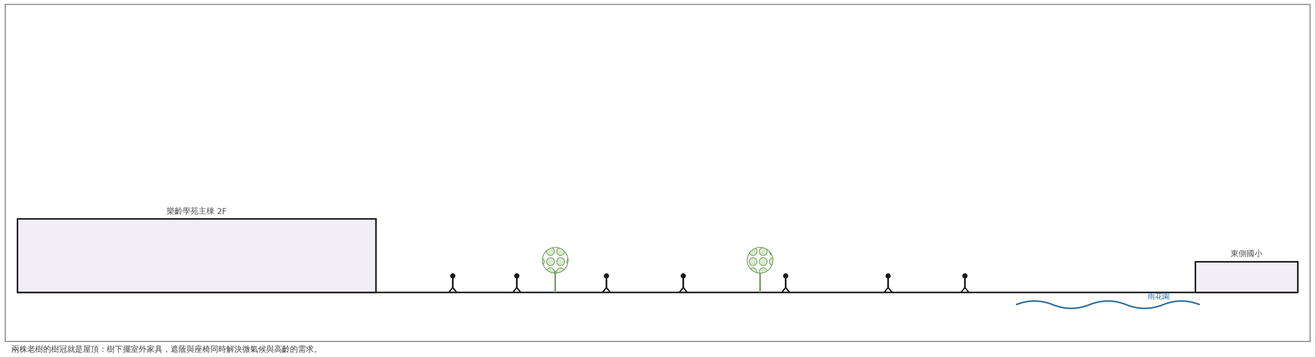

兩株老樹的樹冠就是屋頂：樹下擺室外家具，遮蔭與座椅同時解決微氣候與高齡的需求。
量體只有 2 層、容積只用 58.9%——把地留下來，正是本題「微氣候」與「樂齡」的共同答案。

老樹客廳・風與綠的學苑

社區樂齡學苑｜住宅區 40%／120%｜老樹為核心・通風與保水改善微氣候

申論題（30 分）

①說明都市微氣候之形成原因、忽視微氣候所造成之負面影響，以及都市設計可採行之對策。②說明如何以都市設計手法保存空間形式與舊有之都市記憶。

（一）微氣候：成因→影響→對策

成因	高蓄熱材料、人工發熱、綠地不足 加上風場素亂與日照遮蔽
影響	熱島、能耗上升、污染累積、風害 缺綠使生態與保水下降
對策	通風廊道、增綠覆與透水、遮蔭 退縮與棟距、淺色高反射

（二）保存空間形式與都市記憶

1. 紋理與街廓尺度延續：新量體不打斷既有的街道節奏。
2. 視覺廊道與對景：讓記憶中的地標仍然看得見。
3. 新舊量體對話：以高度遞降與材料呼應，而非模仿。
4. 場所精神再現：保留老樹、水圳、地名與事件的詮釋。
5. 活化再利用：讓舊空間仍在被使用，記憶才不會變標本。

本案的記憶載體就是那兩株老樹——保留它，
等於同時回答了微氣候與都市記憶兩題。

（三）小結

微氣候靠藍綠與通風，記憶靠紋理與場所精神；
兩者都不是文字，都必須落在敷地配置上才算數。

本年官方圖說要求｜逐項打勾

- **規劃理念與全區配置**　通風廊道、老樹保留、雨花園、接送彎皆在圖上　✓
- **機能關係圖**　主棟／保健行政／老樹客廳之關係與無障礙動線　✓
- **剖立面**　A-A' 通風與老樹／B-B' 低層化與防淹抬高　✓
- **透視 ≥1**　老樹客廳午後活動，含人物與尺度　✓

數值證據分級（本張圖）

題目給定：40×55＝2,200 ㎡、40%／120%、老樹兩株、20 M 道路、夏西南/冬東北
圖推概算：老樹位置與冠幅依題圖示意（未標尺寸）
自訂方案：量體尺寸、樓層、抬高 0.5 M、雨花園、通風廊道寬度、不設地下室
題目未指定：空間項目面積、停車位數、高度上限 → 圖上明寫未指定

交卷前：圖名・比例尺・指北・剖面標高數字、
透視有人物、每條算式數字與圖上一致、
題目點名條件逐條指得出位置。

法規檢核｜法源→本案落點

法源（簡稱）	要求	本案落點
技則 綠建築基準	通風、綠化、基地保水改善微氣候	通風廊道＋複層綠覆＋透水鋪面
技則 §302	建築基地綠化量	老樹保留＋複層植栽，一樓留土植穴
技則 §305	基地保水	透水鋪面＋雨花園為保水設施
技則 §4-3	雨水貯集：基地面積×0.045 m³/㎡	2,200×0.045＝99 m³
技則 §39-1	日照：不使鄰地冬至日照<1hr	僅 2 層、退讓充足，無遮蔽疑慮
老人福利法・精神	高齡友善與長者照顧	近保健室、平緩坡道、共餐共學
無障礙設計規範	全程無障礙、防滑	入口無高差、坡度依規範
樹木保護自治條例	受保護樹木原地保留	老樹兩株依地方條例檢討

※ 條號僅供本課查核；考場圖上寫簡稱即可，不背條號。

課題→對策→效益（三行原則）

課題｜微氣候是申論主題，圖上必須看得見
對策｜留西南—東北通風廊道貫穿基地，量體收在西北，東南整片留綠
效益｜申論講的每一項對策，在配置圖上都指得出位置

課題｜老樹兩株容易在配置與施工中犧牲
對策｜建築退出樹冠投影範圍，樹下設室外家具為戶外核心，不設地下室
效益｜老樹從限制變成本案的主角與記憶載體

課題｜舊社區排水老舊、暴雨會淹
對策｜地面層抬高 +0.5 M、透水鋪面、雨花園滯蓄後放流，並不設地下室
效益｜從源頭避開風險，而不是事後加抽水機

課題｜高齡使用者的安全與便利
對策｜單層化動線、近電梯、平緩坡道、防滑鋪面、保健室鄰近活動區
效益｜樂齡不是加幾支扶手，是整條動線的設計

基地核對｜與官方底圖疊合


道路	北側 20 M 道路	✓ 未新增、未拓寬
國小	東側，基地外	✓ 位置未移，接送時段錯開
市場	附近，步行可及	✓ 以次入口銜接，未虛構距離
老樹	基地內兩株	✓ 原地保留，建築退出樹冠投影
地形	略平坦，高差約 0.5 M	✓ 未虛構坡地
界線	矩形 40×55，無凹口	✓ 量體全在界內，不設地下室

量體計算式（逐行可校核）

A ＝ 40 × 55 ＝ 2,200 ㎡〔題目給定〕
B 上限 ＝ A×40% ＝ 880 ㎡　F 上限 ＝ A×120% ＝ 2,640 ㎡（低容積）
投影 B ＝ 主棟 480＋保健行政 168 ＝ 648 ㎡　建蔽 ＝ 29.5% ≦ 40% ✓
G ＝ 480×2F＋168×2F ＝ 960＋336 ＝ 1,296 ㎡　容積率 ＝ 58.9% ≦ 120% ✓
容積用量 ＝ 1,296 / 2,640 ＝ 49.1%（刻意低層化，換取戶外與綠地）
開挖 D ＝ 0 ㎡　開挖率 ＝ 0%（本案不設地下室；淹水潛勢＋容積用量低）
雨水貯集 ＝ 2,200 × 0.045 ＝ 99 m³（技則 §4-3）
戶外：老樹客廳 約 600 ㎡＋雨花園 約 120 ㎡〔方案〕

① 基地硬條件與環境

基地　△ 正文未給面積；依題圖以兩矩形相加量取 ≒ 5,806 ㎡
〔圖推概算〕→ B≤2,322 ㎡、F≤11,612 ㎡
分區　住商混合　建蔽 40%／容積 200%
涵構　邊界凹口「外」有一層三合院（歷史建物）與前埕
東側基地「內」另有捷運出口（題目給定）
基地內既有樹木
都審／題目　須留 3.6 M 無遮簷人行道（題目給定）
⚠ 停止沿用舊值 A＝2,000 ㎡／B＝800／F＝4,000（非原題）。
⚠「歷史建物」不等於已完成法定歷史建築登錄。

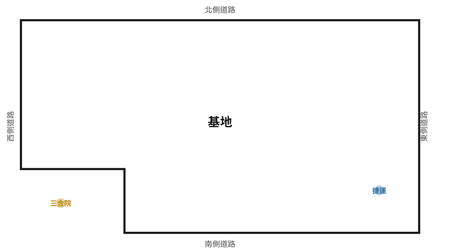

② 英雄條件・課題與對策

英雄條件：三合院前埕＋老樹＋捷運出口（三者串一條線）

課題 1　歷史三合院在凹口外，新量體易壓迫
對策　前埕側低層退讓、留視覺廊道；新舊對話而非比高
課題 2　捷運出口在基地內，人流從東南進入
對策　以文創公共動線串聯：前埕 → 600 ㎡ 廣場 → 捷運出口
課題 3　600 ㎡ 室外多功能廣場要能前臨時展
對策　置北側中段、無建物、鄰咖啡餐廳，與 3.6 M 人行道連成活動帶
課題 4　地下停車 120 輛開挖面積大，恐傷老樹與三合院
對策　開挖退離凹口側與樹群，車道口設東側避開主廣場




細圖示意，不代表比例；正圖見中模配置。

③ 空間需求・量體與開放空間

法規檢核（A/B/G/F/D 五帳）


項目	法定	本案	
基地 A	圖推概算	**≒5,806 ㎡**	△
建蔽率	40%	**33.9%**	✓
建築面積 B	≤2,322 ㎡	**1,968 ㎡**	✓
容積率	200%	**89.3%**	✓
計容積 F	≤11,612 ㎡	**5,184 ㎡**	✓
開挖率 D/A	未給上限	**59.8%**	—

題目空間項目加總 ＝ 800+90+200+250+60+300+60+200 ＝ 1,960 ㎡
⚠ 2,300 ㎡ 是加計公共服務後的「假設」，非題目給定。
室外多功能廣場 600 ㎡（臨時展場）〔題目給定〕
地下停車 120 輛（含 1 裝卸貨）＋機車 25〔題目給定〕
地面公共腳踏車位〔題目給定〕
△ D/H≒2 為設計分析假設，非法規要求。

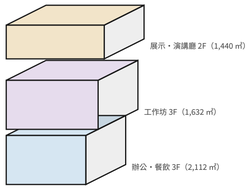


④ 人車動線・防災與管理

人行　主入口設北側接 3.6 M 人行道；動線串前埕、廣場與捷運出口。
車行　卸貨與車道口設東側，鄰開三合院側與主廣場。
停車　B1–B2 汽 120（含 1 裝卸貨）＋機 25〔題目給定〕；
地面另設公共腳踏車位。
保存　三合院在基地外；以低層退讓與視覺廊道呼應，不占用其前埕。
樹木　基地內既有樹木本案選擇原地保留（方案；原題亦准移植）。
防災　600 ㎡ 廣場為無建物避難集結地；B1 兼防空避難。
管理　展演與工作坊可分時段開放；餐廳咖啡對外營業獨立出入。

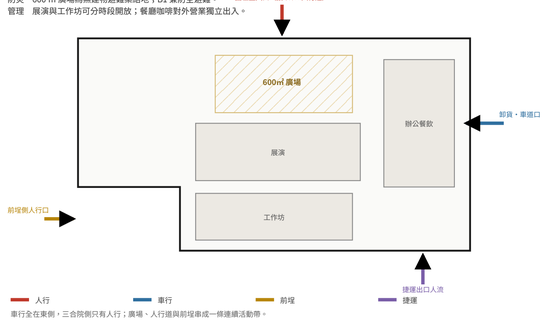


車行全在東側，三合院側只有人行；廣場、人行道與前埕串成一條連續活動帶。

全區配置與地面層景觀（含開挖範圍）

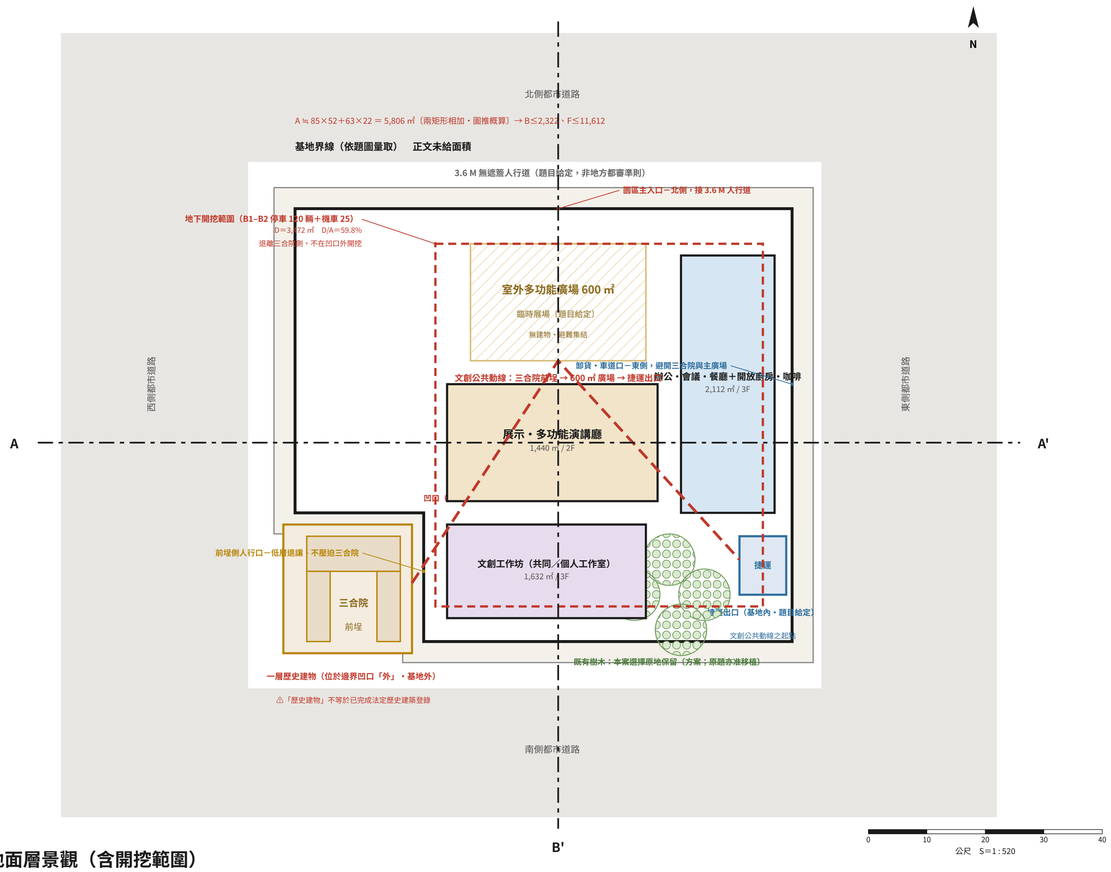

A-A' 剖立面（東西向・證明新舊對話與 D/H 圍塑）

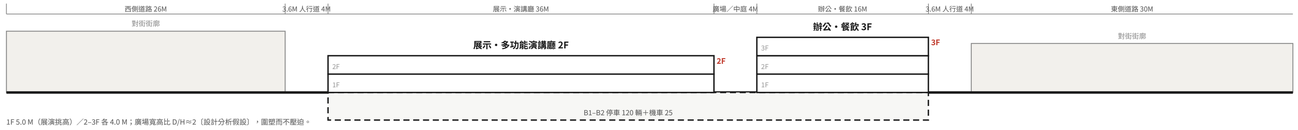


1F 5.0 M（展演挑高）／2–3F 各 4.0 M；廣場寬高比 D/H≒2（設計分析假設），圍塑而不壓迫。

B-B' 剖立面（南北向・證明對三合院之低層退讓）



面三合院一側降為 2 層並退 3.6 M 人行道；三合院僅一層，新量體以高度遞降與視覺廊道呼應其紋理。

局部透視　600 ㎡ 室外多功能廣場（臨時展期間）

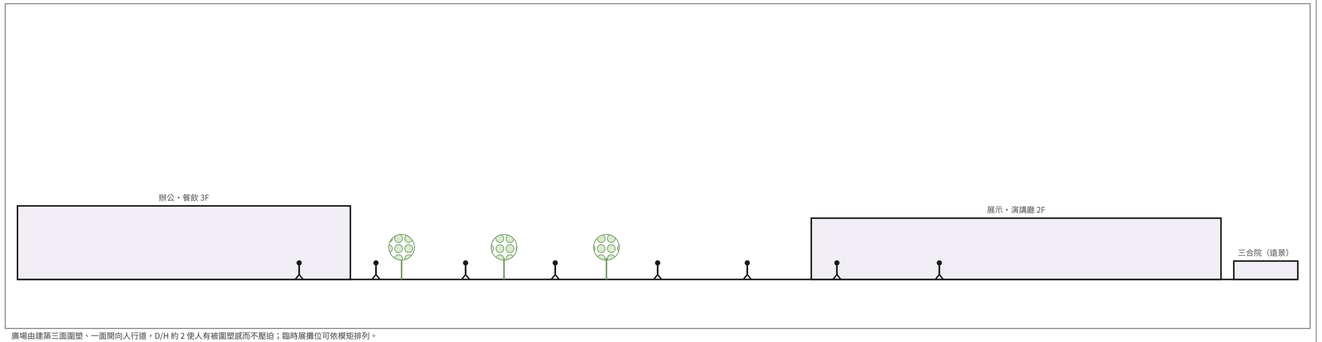

廣場由建築三面圍塑、一面開向人行道，D/H 約 2 使人有被圍塑感而不壓迫；臨時展攤位可依模矩排列。
視線終點是三合院前埕——廣場不只是空地，它是把老屋、老樹與捷運串起來的那一段。

前埕對話・文創廣場

都市中的文創園區｜住商混合 40%／200%｜三合院・老樹・捷運出口串為公共動線

申論題（30 分）

①說明廣場之定義與種類；並描繪一處台灣的廣場（形成原因、變遷、與涵構之互動、不同時間之活動、型態與視野）。②繪該廣場之配置示意圖與剖面示意圖，說明其成功因素與未來期待。

（一）定義與種類

定義	界定明確、供公共活動的都市虛空 以建築或界面圍塑而成
種類	市政／宗教廟埕／商業市集 另有交通集散、社區鄰里
關鍵	不是剩餘空地，而是被設計的空 有邊界、有對景、有活動

（二）成功因素（本題必附配置＋剖面）

圍塑感（D/H 適中）、可及性、人本尺度、混合活動、遮蔭與座椅、與涵構連結（對景為廟或地標）。
剖面要畫出：界面高度、喬木遮蔭、人活動的層次。

⚠ D/H≒2 為設計分析常用參考，非法規規定；
圖上標為「設計分析假設」較穩健。

（三）小結

成功的廣場＝圍塑＋可及＋人本＋混合活動＋涵構連結。
本案文創廣場即以此五項落實：三面圍塑、一面接人行道，對景是三合院前埕，活動由臨時展與咖啡外帶座位供給。

本年官方圖說要求｜逐項打勾

- **全區配置**　含 3.6 M 人行道、600 ㎡ 廣場、開挖範圍、捷運出口　✓
- **廣場配置示意圖＋剖面示意圖**　申論題明文要求，右欄與 B-B' 剖面對應　✓
- **剖立面**　A-A' 新舊對話與 D/H／B-B' 對三合院低層退讓　✓
- **透視 ≥ 1**　廣場臨時展期間，含人物與尺度　✓

數值證據分級（本張圖）

題目給定：40%／200%、3.6 M 無遮簷人行道、廣場 600 ㎡、停車 120＋機 25
圖推概算：A ≒ 5,806 ㎡（兩矩形相加量取；正文未給面積）
自訂方案：量體尺寸、樓層、開挖範圍、既有樹原地保留（原題亦准移植）
題目未指定：高度上限、開挖率上限、綠覆率 → 圖上明寫未指定

交卷前：圖名・比例尺・指北・剖面標高數字、透視有人物、每條算式數字與圖上一致、題目點名條件逐條指得出位置。

法規檢核｜法源→本案落點

法源（簡稱）	要求	本案落點
文資法	維護歷史建物之紋理與環境	前埕與視覺廊道保全，新量體低層退讓
文創產業發展法	文化創意產業之聚落營造	工作坊、展演與餐飲形成產業聚落
都計法 §22	細部計畫定土地使用分區管制	住商混合 40%／200%
通盤檢討辦法	都市設計應表明地下室開挖之限制	開挖退離凹口側，D/A≒59.8%
技則 §162-1-3	法定停車空間得不計入容積	B1–B2 停車不計入 F
技則 §302／§305	綠化量與基地保水	既有樹保留＋廣場透水鋪面
技則 §4-3	雨水貯集：基地面積×0.045 m³/㎡	5,806×0.045 ≒ 261.3 m³
樹木保護自治條例	受保護樹木原地保留	既有樹依地方條例檢討（本案保留）

※ 條號僅供本圖查核；考場圖上寫簡稱即可，不背條號。

課題→對策→效益（三行原則）

課題｜正文未給基地面積，數字難所依據
對策｜以兩矩形相加由題圖量取 ≒5,806 ㎡，並在圖上標為圖推概算
效益｜所有比率有同一個可校核的分母，不用舊的 2,000 ㎡

課題｜三合院在凹口外，新量體易壓迫
對策｜面三合院一側降為 2 層、退 3.6 M 人行道、留視覺廊道
效益｜新舊以高度遞降對話，不占用他人前埕

課題｜捷運出口在基地內，人流方向與主入口不同
對策｜以一條文創公共動線串聯前埕、600 ㎡ 廣場與捷運出口
效益｜三個既有條件被同一條動線收成一個系統

課題｜120 輛地下停車開挖大，恐傷老樹
對策｜開挖退離凹口側與樹群，車道口設東側避開主廣場與三合院
效益｜停車的量做到了，保存的姿態也看得見

基地核對｜與官方底圖疊合


凹口	西南邊界凹口，三合院在凹口外	✓保留凹口，未填平、未占用
三合院	一層歷史建物，基地外	✓低層退讓，留視廊，未畫入基地
捷運	東側基地內另有捷運出口	✓已畫出，未遮漏
樹木	基地內既有樹木	✓原地保留（標為方案）
人行道	3.6 M 無遮簷〔題目給定〕	✓環基地連續，非都審準則
面積	正文未給	✓以兩矩形相加量取並標概算

量體計算式（逐行可校核）

A ＝ 85×52 ＋ (85−22)×22 ＝ 4,420 ＋ 1,386 ＝ 5,806 ㎡（兩矩形相加・圖推概算）
B上限 ＝ A×40% ≒ 2,322 ㎡　F上限 ＝ A×200% ≒ 11,612 ㎡
題目空間項目加總 ＝ 800+90+200+250+60+300+60+200 ＝ 1,960 ㎡〔題目給定〕
投影 B ＝ 720＋544＋704 ＝ 1,968 ㎡　建蔽 ＝ 33.9% ≤ 40% ✓
G ＝ 720×2F＋544×3F＋704×3F ＝ 1,440＋1,632＋2,112 ＝ 5,184 ㎡
容積率 ＝ 5,184 / 5,806 ＝ 89.3% ≤ 200% ✓（容積刻意不用滿，換取廣場與退讓）
室外多功能廣場 ＝ 30M × 20M ＝ 600 ㎡ ✓〔題目給定〕
開挖 D ＝ 56M × 62M ＝ 3,472 ㎡　開挖率 ＝ 59.8%〔題目未給上限〕
雨水貯集 ＝ 5,806 × 0.045 ≒ 261.3 m³（技則 §4-3）

① 基地硬條件與環境


基地　60 M × 32 M ＝ 1,920 ㎡〔題目給定〕
分區　住宅區　建蔽 50%／容積 200%
南（長邊 60 M）　隔 9 M 巷對三角形社區公園 → 主開放面
西／西南（短邊）　臨 40 M 道路，對側住商 7–12 層 → 主人行入口
東　4–5 層老舊公寓 → 量體退讓，檐高呼應
北　隔 6 M 巷 → 車行、服務、垃圾清運次入口
氣候／水文　夏西南、冬東北；排水老舊、暴雨淹水
⚠ 公園在基地外、隔 9 M 道路——寫「以安全穿越及視線連接公園」，
不可寫成「公園即中心之前庭」。

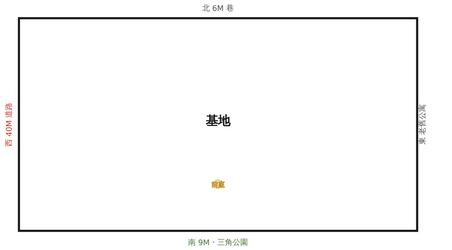

② 英雄條件・課題與對策

英雄條件：南面三角形社區公園

課題 1　基地只有 1,920 ㎡，卻要 900 坪機能
對策　900 坪＝2,975.21 ㎡；3,300÷960＝3.44 → 約 4 層
⚠ 三層湊建蔽僅 2,880 ㎡，不能說「3–4 層皆足」
課題 2　親民與私密同時要（共餐 vs 緊急安置）
對策　前庭與大廳朝南全開放；緊急安置置東端，
北側 6 M 巷設專用獨立出入口，與展演分流
課題 3　排水老舊、暴雨淹水
對策　地面層抬高 +0.6 M、透水鋪面、雨花園、屋頂滯洪
課題 4　住宅區要辦集會、展演
對策　先確認住宅區容許使用；集會類二方向避難、
直通避難層出入口，控制步行距離

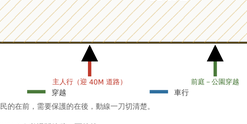


縮圖示意，不代表比例；正圖見中欄配置。

③ 空間需求・量體與開放空間

法規檢核（A/B/G/F/D 五帳）


項目	法定	本案	
基地 A	—	**1,920 ㎡**	—
建蔽率	50%	**43.3%**	✓
建築面積 B	≤960 ㎡	**832 ㎡**	✓
容積率	200%	**173.3%**	✓
計容積 F	≤3,840 ㎡	**3,328 ㎡**	✓
開挖率 D/A	未給上限	**48.8%**	—

課程／親子／共餐／講座／祈禱室 600 坪＝1,983.5 ㎡
多媒體展示販售 200 坪＝661.2 ㎡｜營運辦公 100 坪＝330.6 ㎡
合計 900 坪 ＝ 2,975.21 ㎡〔題目給定；1 坪＝400/121〕
本案 3,328 ㎡ 為方案（含緊急安置、動線與服務）
⚠ 以 3.3 概算 2,970 ㎡ 須標「約」。
⚠ 祈禱空間不宜假設同一宗教朝向，應具包容彈性。

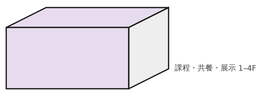


④ 人車動線・防災與管理

人行　主人行入口迎西側 40 M 道路（大眾運輸入流）；
大廳與前庭朝南，以行穿線與路口緩衝安全連接公園。
車行　北側 6 M 巷道進出，與南面人流完全分離。
服務　垃圾清運、供應走北側；緊急安置專用出入口亦在北側東端。
停車　地面自行車 ≥10；地下 汽 12＋機 10〔題目給定〕。
防災　三層次——B1 防空避難／南側前庭地震集合／地面抬高防洪。
避難　集會類二方向避難、直通避難層出入口、控制步行距離。
無障礙　全程無障礙（含長者、孕婦、騎樓 戶誤（北 6M）
管理　展演與私密服務分流；前庭可獨立於室內開放。

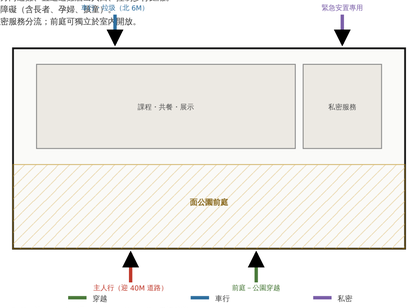

南面全開放、北面全服務：親民的在前，需要保護的在後，動線一刀切清楚。

全區配置與地面層景觀（含開挖範圍）

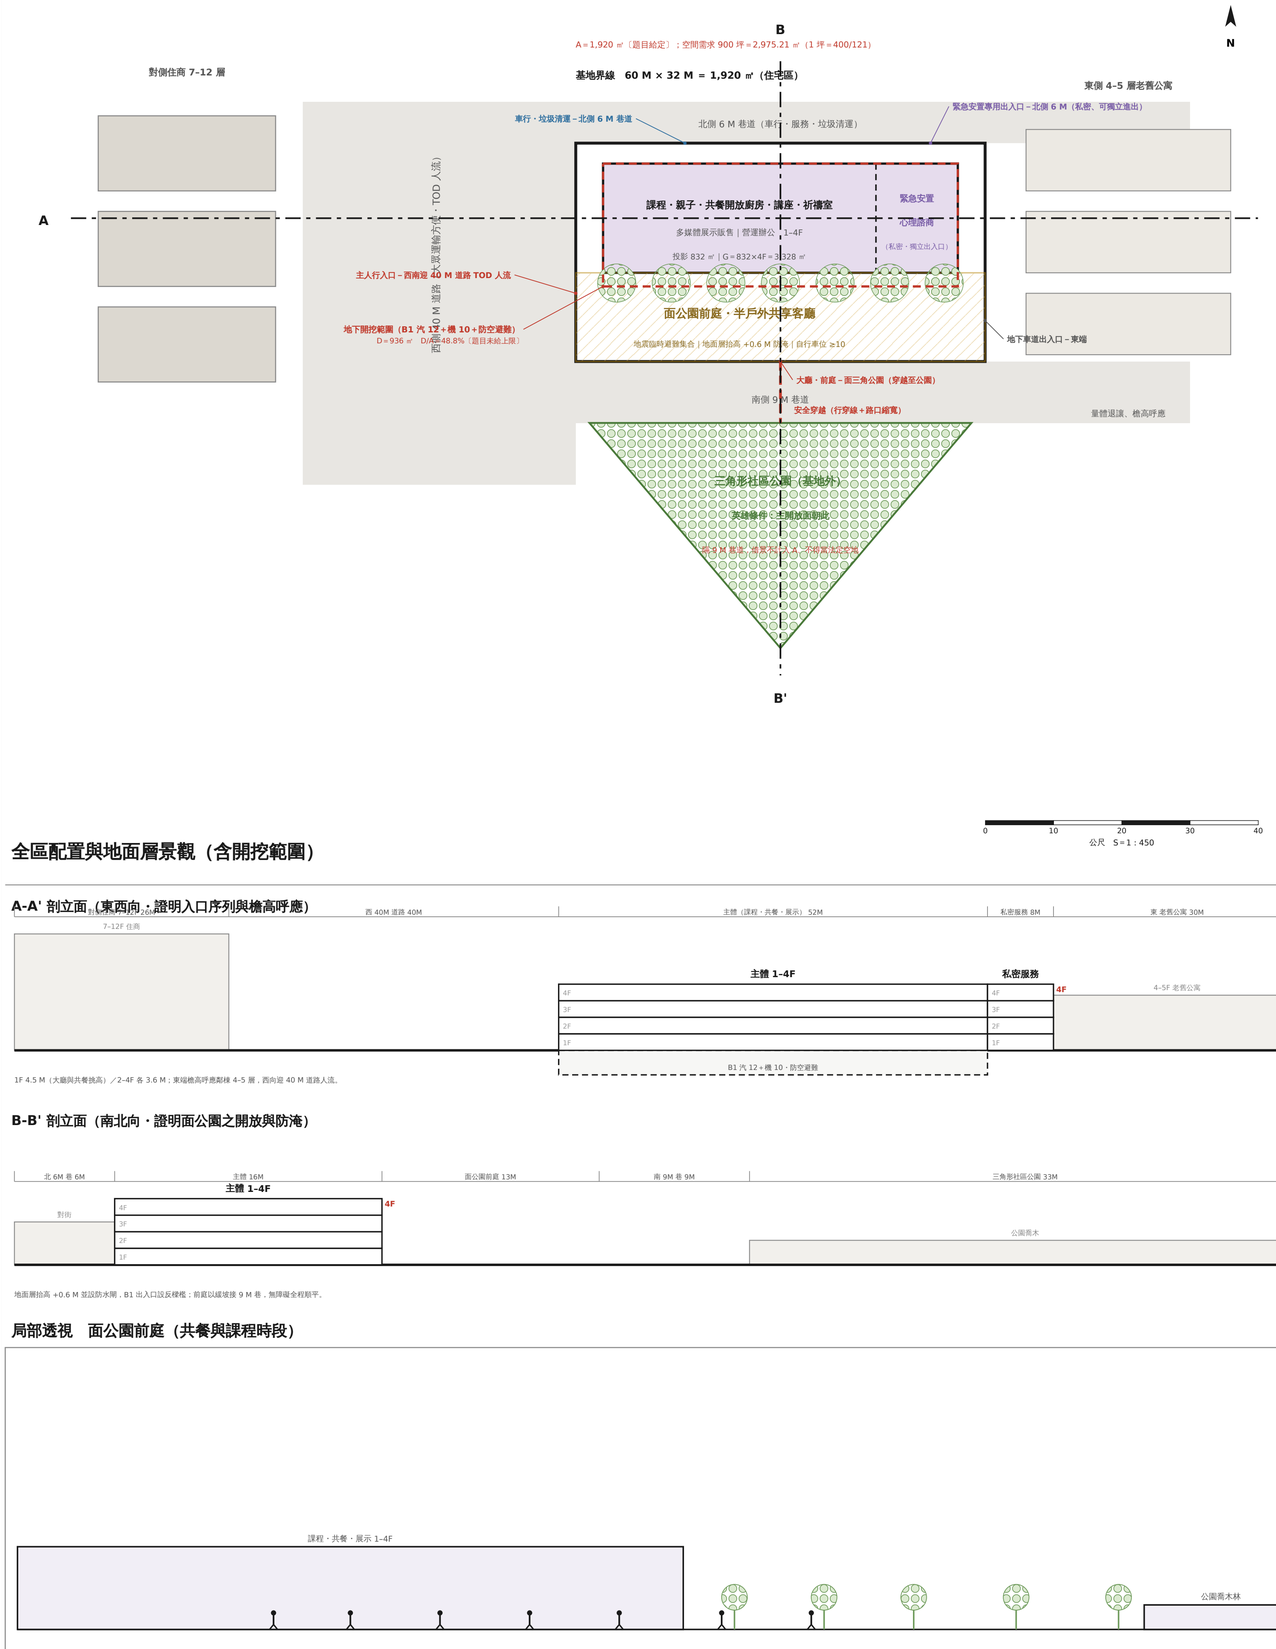


A-A' 剖立面（東西向・證明入口序列與檐高呼應）

1F 4.5 M（大廳與共餐挑高）／2–4F 各 3.6 M；東端檐高呼應鄰棟 4–5 層，西向迎 40 M 道路入流。

B-B' 剖立面（南北向・證明面公園之開放與防淹）

地面層抬高 +0.6 M 並設防水閘，B1 出入口設反樓梯；前庭以緩坡接 9 M 巷，無障礙全程順平。

局部透視　面公園前庭（共餐與課程時段）

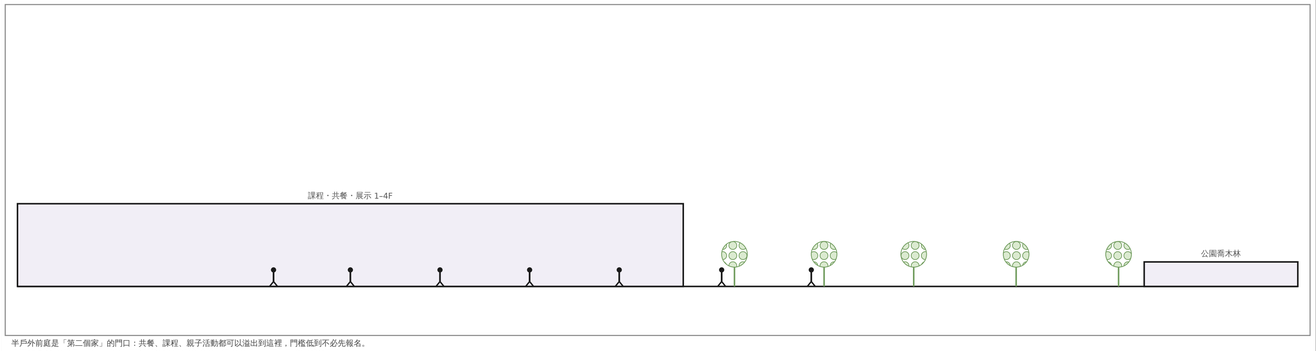

半戶外前庭是「第二個家」的門口：共餐、課程、親子活動都可以溢出到這裡，門檻低到不必先報名。
公園在 9 M 巷的另一側——以行穿線與路口緩寬安全連接，視線連續，但不把對街畫成自家庭院。

公園客廳・第二個家

新住民文化交流中心｜住宅區 50%／200%｜南面三角公園・私密服務在後

申論題（30 分）

說明「都市縫合」之意涵，並以大眾運輸導向發展（TOD）
為例，說明車站周邊如何透過都市設計手法縫合被
切割的都市紋理。

（一）都市縫合的三個尺度

路網	接回被切斷的人行與自行車路徑 本案 40 M 道路側設連續人行
街廓	量體退讓形成連續開放空間 南側前庭接公園
界面	一樓活化、騎樓與遮蔭連續 大廳與共餐面街開放

（二）TOD 的縫合手法

1. 站區 500 M 內提高混合使用與步行可及性。
2. 以立體或平面人行連通跨越幹道，縮短繞行。
3. 車站前廣場作為節點，串聯公車、自行車與周邊公共設施。
4. 停車由路側改為集中立體，把地面還給人。

> ⚠「**縫合**」須有實際可走的路徑；
> **視線連通不等於可及性，圖上要畫得出穿越點。**

（三）小結

縫合不是把兩塊地畫成同一種顏色，而是讓人能走過去。
本案的縫合證據，就是那條穿越 9 M 巷通往公園的行穿線。

本年官方圖說要求｜逐項打勾

構想圖（含防救災、垃圾清運） 三層次防災與垃圾清運與服務動線標示	✓
配置圖 1/300 量體、前庭、開挖、自行車位與出入口	✓
剖立面 A-A' 入口序列與檐高／B-B' 面公園與防淹抬高	✓
小透視 面公園前庭，含人物與尺度	✓

數值證據分級（本張圖）

題目給定：60×32＝1,920 ㎡、50%／200%、900 坪機能、停車汽12機10、自行車≥10
換算：900 坪 × 400/121 ＝ 2,975.21 ㎡（以 3.3 概算 2,970 須標「約」）
自訂方案：樓層 4F、量體尺寸、抬高 0.6 M、開挖範圍、私密區位置
題目未指定：高度上限、開挖率上限、綠覆率 → 圖上明寫未指定

交卷前：圖名・比例尺・指北・剖面樓高數字、
透視有人物、每條算式數字與圖上一致、
題目點名條件逐條指得出位置。

法規檢核｜法源→本案落點

法源（簡稱）	要求	本案落點
都計法・土管	住宅區容許使用之檢討	公益服務設施須先確認為容許使用
技則 集會類	二方向避難、直通避難層出入口	講座展演區設二方向避難
技則 §162-1-3	法定停車空間得不計入容積	B1 汽 12＋機 10 不計入 F
技則 §141	防空避難設備	B1 兼防空避難
技則 §302／§305	綠化量與基地保水	前庭透水鋪面＋雨花園＋屋頂綠化
技則 §4-3	雨水貯集：基地面積×0.045 m³/㎡	1,920×0.045＝86.4 m³
技則 §39-1	日照：不使鄰地冬至日照<1hr	東側退讓，檐高呼應 4–5 層
無障礙設計規範	全程無障礙	前庭緩坡、入口無高差、防滑

※ 條號僅供本課查核；考場圖上寫簡稱即可，不背條號。

課題→對策→效益（三行原則）

課題｜1,920 ㎡ 要放 900 坪機能，樓層一定要算清楚
對策｜2,975.21÷960＝3.10；含服務取 3,300×960＝3.44 → 約 4 層
效益｜「3–4 層皆足」是錯的；三層湊建蔽僅 2,880 ㎡

課題｜親民與私密兩種需求互相干擾
對策｜前庭與大廳朝南全開放；緊急安置與心理諮商置東端，北側專用出入口
效益｜求助的人不必穿過熱鬧的共餐區

課題｜排水老舊、暴雨會淹
對策｜地面層抬高 +0.6 M＋防水閘、B1 口反樓梯、透水鋪面與雨花園、屋頂滯洪
效益｜淹水不進室內、不進地下，避難層永遠可用

課題｜公園在對街，容易說當自家前庭
對策｜以行穿線與路口緩寬安全連接，視線連續；A 與法定空地均不含公園
效益｜連接是真的走得過去，不是圖面上的顏色相連

基地核對｜與官方底圖疊合


道路	西 40M／北 6M 巷／南 9M 巷	✓ 未新增、未拓寬
公園	南側三角形，隔 9M 巷、基地外	✓ 借景不計入 A，畫出穿越
鄰棟	東側 4–5 層老舊公寓	✓ 位置未移，本案退讓呼應
對側	西側住商 7–12 層	✓ 剖面畫出，未忽略高差
形狀	矩形 60×32，無凹口	✓ 量體與開挖均在界內
氣候	夏西南／冬東北	✓ 南面開口迎夏風，北面服務擋冬風

量體計算式（逐行可校核）

A ＝ 60 × 32 ＝ 1,920 ㎡〔題目給定〕
B上限 ＝ A×50% ＝ 960 ㎡　F上限 ＝ A×200% ＝ 3,840 ㎡
需求 ＝ (600＋200＋100) 坪 × 400/121 ＝ 900 × 3.3058 ＝ 2,975.21 ㎡〔題目給定〕
樓層 ＝ 2,975.21 ÷ 960 ＝ 3.10；含服務取 3,300 ÷ 960 ＝ 3.44 → 約 4 層
△ 三層湊建蔽僅 960×3 ＝ 2,880 ㎡ < 2,975.21，故三層不足
投影 B ＝ 52M × 16M ＝ 832 ㎡　建蔽 ＝ 43.3% ≦ 50% ✓
G ＝ 832 × 4F ＝ 3,328 ㎡　容積率 ＝ 173.3% ≦ 200% ✓
開挖 D ＝ 52M × 18M ＝ 936 ㎡　開挖率 ＝ 48.8%〔題目未給上限〕
雨水貯集 ＝ 1,920 × 0.045 ＝ 86.4 m³（技則 §4-3）

① 基地硬條件與環境

基地　完整街廓 約 200 M × 200 M ＝ 40,000 ㎡（4 公頃・機關用地）
周界　西 15 M、東 30 M、南北各 10 M 道路
地形　北高南低，坡度約 1%〔題目給定〕
涵構　周邊低矮社區依危老往高層，西側已 12–16 層
配比　校舍 30%／運動 30%／綠地步道 40%
〔土地使用參考原則，非建蔽率、非樓地板需求〕
團說配分　分區規劃 25／國小規劃設計 35／透視 10
⚠ 建蔽率與容積率題目未給 → 不得自行發明，圖上明寫未指定。
⚠ 109 年當時危老「時程獎勵」為 8%（109.5.12–110.5.11），非歸零。

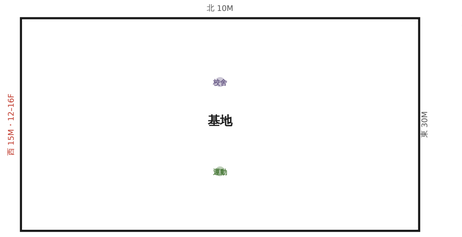

② 英雄條件・課題與對策

英雄條件：4 公頃完整街廓＋西側 12–16 層高層

課題 1　4 公頃太大，先設計會失去秩序
對策　先 zoning 再設計：教學核／運動區／社區共享／綠環
課題 2　西側 12–16 層遮擋寧日照
對策　校舍低層（主要教學建築原則不超過 3 層）並東移；
西側留 15 M 綠環林帶緩衝，教室南向採光
課題 3　北高南低 1%，整地與排水
對策　運動場置較平處、順坡整地、設截水溝，無障礙順平
課題 4　幼兒園、長青學院與國小共用，管理與安全
對策　幼兒園獨立出入口在南；長青學院置東緣，假日可單獨開放




縮圖示意・不代表比例；正圖見中欄配置。

③ 空間需求・量體與開放空間

空間需求驗算（題目給定數量）


項目	法定	本案	
基地 A	—	**40,000 ㎡**	—
普通教室	18 間×72	**1,296 ㎡**	✓
專科教室	8 間×108	**864 ㎡**	✓
服務行政	20 單元	**1,440 ㎡**	✓
小計	≥3,600 ㎡	**3,600 ㎡**	✓
建蔽／容積	題目未給	**未指定**	—

幼兒園活動室 ≥450 ㎡；長青學院 660 ㎡〔題目給定〕
投影 B＝2,328 ㎡；總樓地板 G＝5,256 ㎡（另計走廊）
題定尺寸：200 M 跑道、兩面 16×28 M 籃球場
走廊淨寬：單邊 ≥2.5 M、中央 ≥3 M；樓梯 ≥1.4 M；逃生距離 ≤50 M
停車 100 輛；地面至少 20〔題目給定〕；
⚠ 並非其餘 80 輛一律地下——本案地面 25＋地下 75。

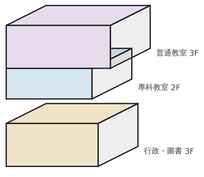


④ 人車動線・防災與管理

通學　主入口設北側 10 M，人車分道；綠環步道即通學步道。
接送　東側 30 M 設地面接送車道與等待彎，不進教學核。
服務　廚餐、垃圾、供應走西側 15 M，與學童動線完全分離。
分齡　幼兒／低年級／高年級分區，幼兒園南側獨立出入口。
防災　中庭與運動場內場草地為地震臨時避難集合場。
各棟二方向避難、逃生距離 ≤50 M。
排水　順坡整地，運動場周邊設截水溝；綠環為滲帶。
共享　長青學院置東緣，假日可單獨開放，校園核心可關閉。

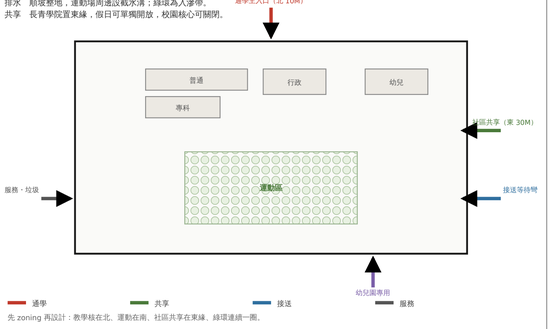


先 zoning 再設計：教學核在北、運動在南、社區共享在東緣、綠環連續一圈。

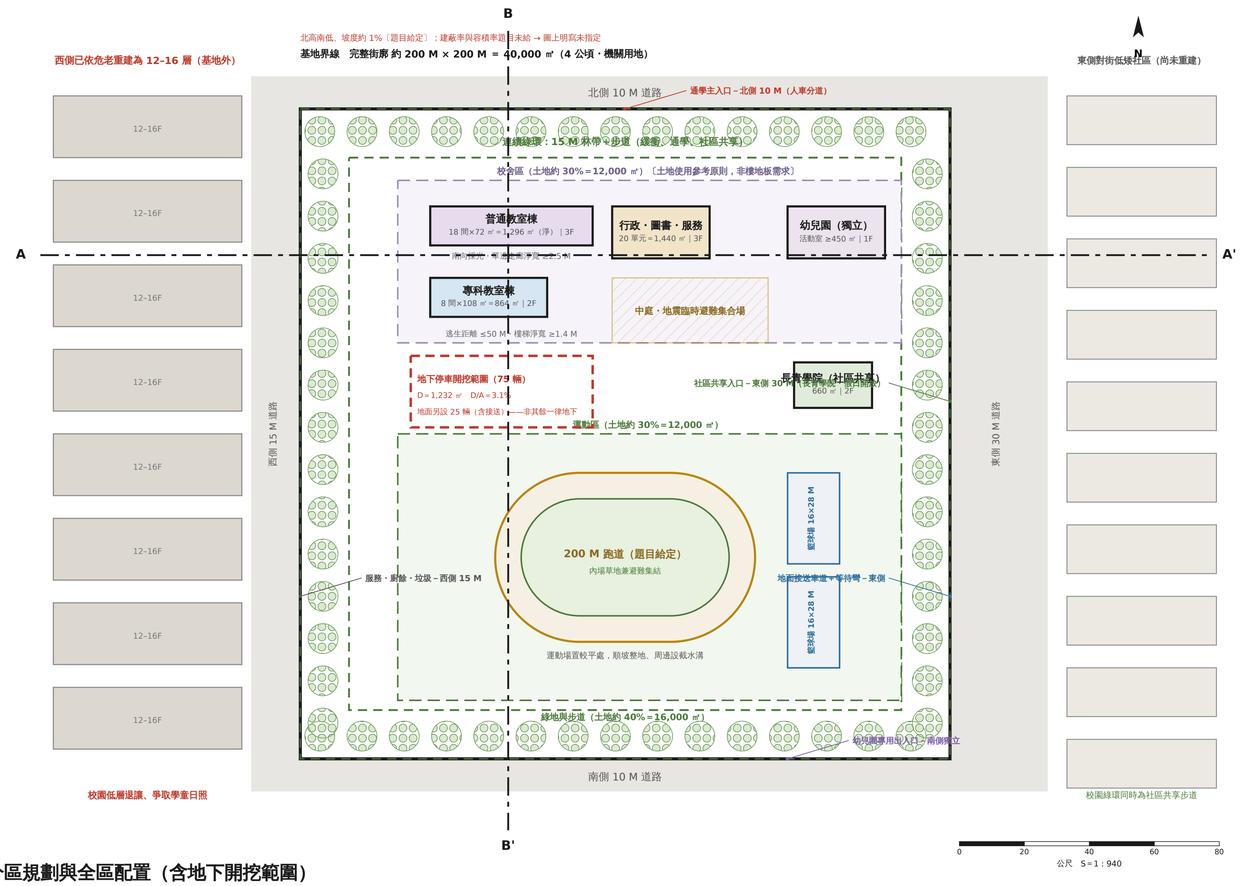

分區規劃與全區配置（含地下開挖範圍）

A-A' 剖立面（東西向・證明對西側高層之日照退讓）

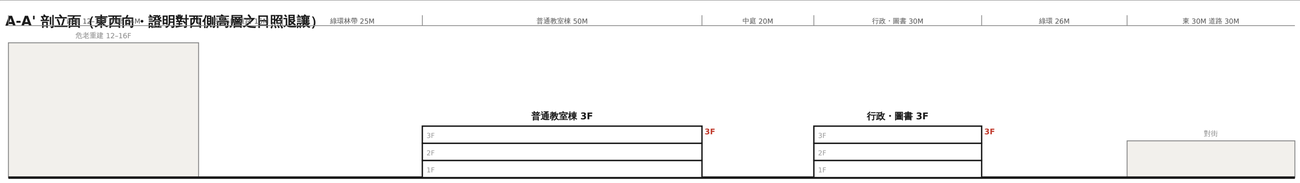


主要教學建築原則不超過 3 層；西側留 15 M 綠環林帶緩衝，教室南向採光，不與高層比高。

B-B' 剖立面（南北向・證明北高南低 1% 與運動場整地）



北高南低坡約 1%（200 M 落差約 2 M）：教學核置北側較高處，運動場置南側較平處順坡整地並設截水溝。

局部透視　中庭望向普通教室棟（下課時段）

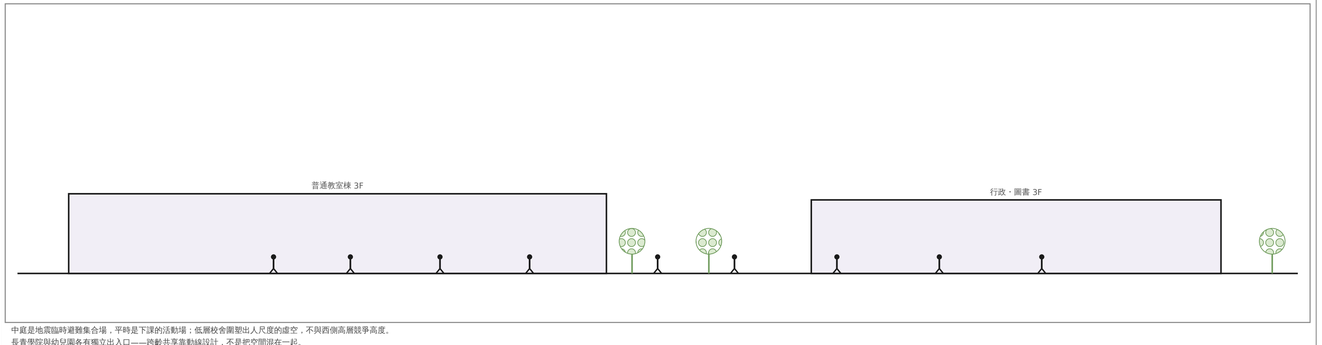

中庭是地震臨時避難集合場，平時是下課的活動場；低層校舍圍塑出人尺度的虛空，不與西側高層競爭高度。
長青學院與幼兒園各有獨立出入口——跨齡共享靠動線設計，不是把空間混在一起。

開放校園・跨齡共享

都市國民小學新校園｜機關用地 4 公頃｜北高南低 1%・西鄰 12–16 層

申論題（30 分）

比較《都市更新條例》與《都市危險及老舊建築物加速重建條例》之異同，並說明二者在都市空間改造上的角色與限制。

（一）異同比較

範圍	都更劃更新單元／危老就個別基地 危老免劃更新地區
程序	都更可權利變換／危老為重建計畫 權利變換非都更唯一途徑
誘因	皆有容積獎勵與稅捐減免 109 年時程獎勵為 8%

（二）角色與限制

都更適合面的整體規劃：可調整公設、路型與開放空間。
危老適合點的加速重建：耐震與安全優先，但難改都市紋理。
限制：危老常含體土地及合法建物所有權人同意；
屋齡 30 年以上並非唯一門檻，另有合法性與安全評估。

⚠ 答 109 年舊題須用當年版本：時程獎勵 8%。
現行（114.5.12 起）時程獎勵已歸零，改為規模獎勵。

（三）小結

「都更管面、危老管點」只能當概念提示，不是法定分工。
本案校園緊鄰危老重建之 12–16 層——這正是點式重建改不了天際線與日照的限制，需由校園以低層退讓來承接。

本年官方團說要求｜逐項打勾

- **分區規劃（25 分）**　校舍／運動／綠地步道三分區與綠環，依土地使用參考原則　✓
- **國小規劃設計（35 分）**　教室數量、走廊淨寬、逃生距離、分齡分區管標示　✓
- **透視（10 分）**　中庭望教室棟，含人物與尺度　✓
- **剖立面**　A-A' 對西側高層退讓／B-B' 北高南低 1%　✓

數值證據分級（本張圖）

題目給定：4 公頃、道路寬、坡度 1%、教室數量與單元、200 M 跑道、16×28 球場、停車 100
團推概算：街廓以 200×200 概估（題目稱「約 4 公頃」）
自訂方案：量體尺寸、樓層、三分區邊界、地面 25／地下 75 之停車配置
題目未指定：建蔽率、容積率、開挖率上限 → 圖上明寫未指定

交卷前：圖名・比例尺・指北・剖面標高數字、
透視有人物、每條算式數字與圖上一致、
題目點名條件逐條指得出位置。

法規檢核｜法源→本案落點

法源（簡稱）	要求	本案落點
都計法 §22	細部計畫定公共設施用地	機關用地（學校）；建蔽容積題目未給
國民小學設備基準	教室、專科、行政單元面積	18×72＋8×108＋20 單元＝3,600 ㎡
技則 §92／§93	走廊淨寬與樓梯	單邊 ≥2.5 M、中央 ≥3 M、樓梯 ≥1.4 M
技則 防火避難	逃生距離與二方向避難	逃生距離 ≤50 M，各棟二方向
技則 §39-1	日照：不使鄰地冬至日照<1hr	校舍 3 層低層，東移並留 15 M 綠環
技則 §302／§305	綠化量與基地保水	綠環林帶＋運動場草地入滲
技則 §141	防空避難設備	地下停車兼防空避難
無障礙設計規範	全程無障礙	順坡整地使 1% 坡度可無障礙通行

※ 條號僅供本庫查核；考場圖上寫簡稱即可，不背條號。

課題→對策→效益（三行原則）

課題｜4 公頃完整街廓，先畫建築一定失序
對策｜先 zoning：教學核在北、運動在南、社區共享在東緣、綠環連續一圈
效益｜大基地有結構，每一棟都說得出為何在此

課題｜西側 12–16 層高層遮擋寧童日照
對策｜主要教學建築原則不超過 3 層並東移，西側留 15 M 綠環林帶
效益｜不與高層比高，改用距離與朝向爭日照

課題｜北高南低 1%，整地與排水易失控
對策｜運動場置南側較平處順坡整地，周邊設截水溝，全程無障礙順平
效益｜地形不是問題，是分區的依據

課題｜跨齡共用（幼兒／國小／長青）管理困難
對策｜幼兒園南側獨立出入口、長青學院置東緣可單獨開放，核心可關閉
效益｜共享靠動線分離達成，不是把人混在一起

基地核對｜與官方底圖疊合

道路	西 15M／東 30M／南北各 10M	✓ 未新增、未拓寬
街廓	完整街廓，約 4 公頃	✓ 未分割、未跨界
坡向	北高南低約 1%	✓ 剖面標示，未整平為水平
鄰棟	西側 12–16 層在基地外	✓ 位置未移，退讓在本案
跑道	200 M（題目給定）	✓ 尺寸未縮、置較平處
球場	兩面 16×28 M（題目給定）	✓ 數量與尺寸皆符


量體計算式（逐行可校核）

A ＝ 約 200 × 200 ＝ 40,000 ㎡（4 公頃）〔題目稱「約」，屬團推概算〕
土地配比〔參考原則〕：校舍 30%＝12,000／運動 30%＝12,000／綠地步道 40%＝16,000 ㎡
普通教室 ＝ 18 間 × 72 ＝ 1,296 ㎡（淨）
專科教室 ＝ 8 間 × 108 ＝ 864 ㎡　服務行政 ＝ 20 單元 ＝ 1,440 ㎡
小計 ＝ 1,296＋864＋1,440 ＝ 3,600 ㎡ ≥ 題目要求 ✓（另加走廊）
投影 B ＝ 600＋432＋480＋480＋336 ＝ 2,328 ㎡　建蔽 ＝ 5.8%〔題目未給上限〕
G ＝ 1,800＋864＋1,440＋480＋672 ＝ 5,256 ㎡　容積率 ＝ 13.1%〔題目未給上限〕
停車 100 輛：地面 25（含接送）＋地下 75〔方案；題目僅要求地面至少 20〕
開挖 D ＝ 56M × 22M ＝ 1,232 ㎡　開挖率 ＝ 3.1%
雨水貯集 ＝ 40,000 × 0.045 ＝ 1,800 m³（技則 §4-3）

① 基地硬條件與環境

基地　近梯形：北 188 M／南 177 M／深 175 M
A ≒ 31,937.5 ㎡（圖推概算）
分區　機關用地　建蔽 50%／容積 200%〔題目給定〕
北　　20 M 聯外道路（3 M 人行道・服務水準 B）
隔路為大型公園（基地外・使用強度高）
西・南 15 M 社區巷道，無人行道
東　　5 M 防汛道（平時禁汽機車・開放人行自行車）
外接 8 M 綠帶＋溪溝寬 6M 深 3M
氣候　夏 29°C 西南風／冬 16°C／11 月東北季風 23.3 km/h
⚠ 原題明示「基地平緩不淹水」——忠實保留，不改題。

⚠ 公園・防汛道・綠帶・溪溝均在基地外，
不得計入 A 或法定空地；僅景≠用地控制權。

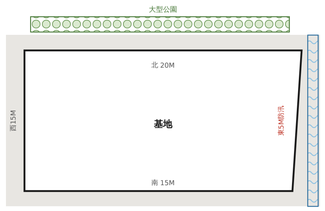

② 英雄條件・課題與對策

英雄條件：北公園＋東溪流，兩個基地外資源

課題1 公園與溪流皆在基地外，且各隔一條路
對策 東北第一象限整塊留為市民廣場，
北以人行穿越接公園、東以緩坡接防汛道。①
課題2 容積僅用 27.4%，易流於空曠無用
對策 廣場需有遮蔭、活動與綠護計畫，
非只畫大片空地。②
課題3 三大機能尺度差異大（體健需挑高）
對策 量體往西、南組織，低層分棟；
體健中心獨立大跨距量體。③
課題4 東側防汛道禁汽機車
對策 車行一律由西側 15M 巷道進出，
防汛道僅作人行自行車銜接。④


編號①–④對應中央配置圖同編號位置。

③ 空間需求・量體與開放空間

法規檢核表（A/B/G/F/D 五帳）

項目	法定	本案	
基地 A	—	**31,937.5 ㎡**	—
建蔽率	50%	**25.4%**	✓
建築面積 B	≤15,968 ㎡	**8,126 ㎡**	✓
容積率	200%	**54.8%**	✓
計容積 F	≤63,875 ㎡	**17,500 ㎡**	✓
開挖率 D/A	未給上限	**36.3%**	—


行政中心　　9,000 ㎡ ÷ 3F ＝ 3,000 ㎡
圖書館＋大會議室 4,500 ㎡ ÷ 2F ＝ 2,250 ㎡〔題目為合計〕
體健中心　　4,000 ㎡ ÷ 2F ＝ 2,000 ㎡（挑高）
入口大廳・連廊　約 850 ㎡〔自訂方案〕
投影合計 B ＝ 8,126 ㎡　→ 建蔽
G＝17,500 ㎡（題目需

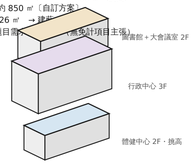

⚠ 不得以 17,500÷3 概算占地：體健中心
之挑高與大跨距須另行驗算。


④ 人車動線・防災與管理

人行　北側市民主入口正對公園，設安全穿越；
東側以緩坡接防汛道之步行自行車系統。
車行　地下車道出入口設西側 15M 巷道；④
卸貨與清潔隊由南側 15M 巷道進出。
東側防汛道全程不作汽機車進出。
停車　地下 汽 90／機 50；地面 自行車 120〔題目給定〕
防災　市民廣場兼地震臨時避難場所；
救災動線由北 20M 路直達廣場，不穿越量體。
水文　生態水池具有效容積與控制出流；
基地不淹水為原題條件，仍分析溪流風險。
管理　廣場全時開放；行政中心分時門禁，
假日僅開放圖書館與體健中心。

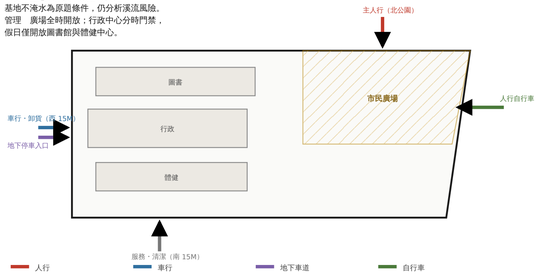


人車分流：車行僅西側進出，北側廣場面全步行；防災時廣場為集結地。

全區配置與地面層景觀

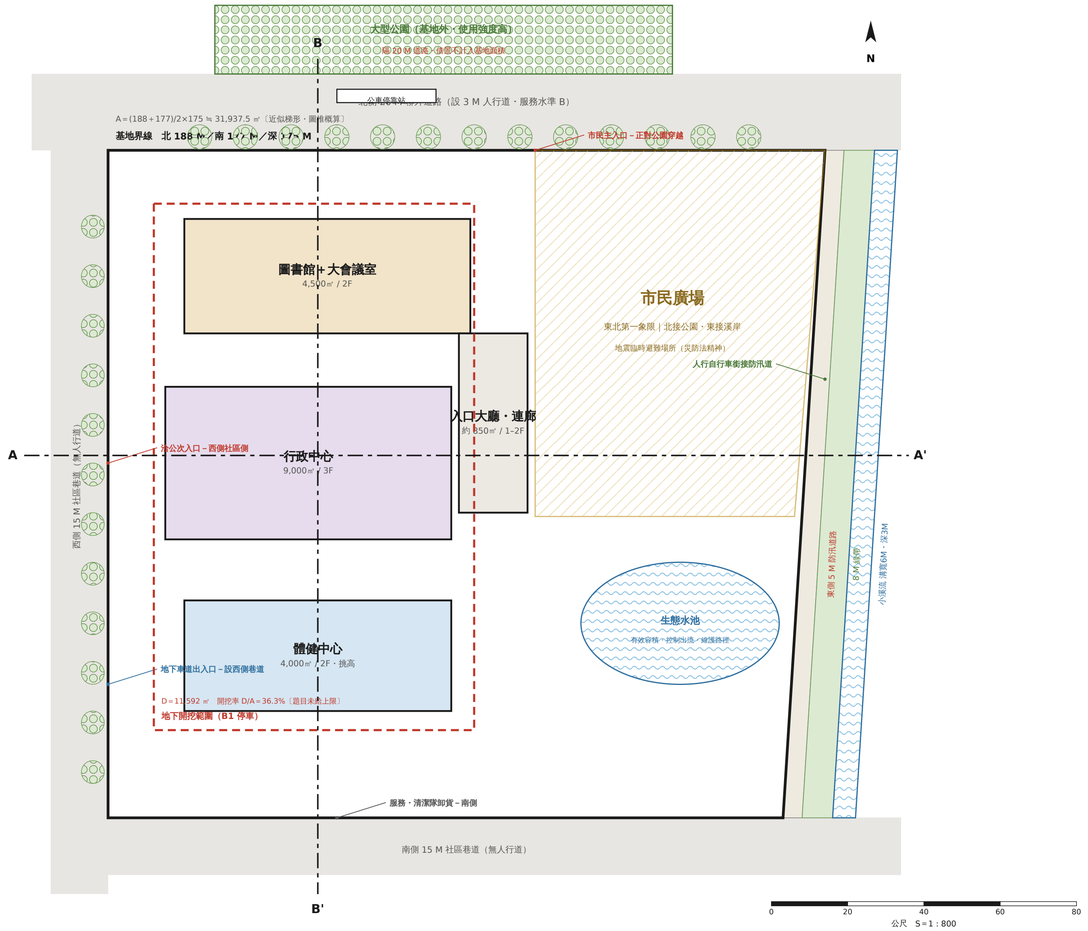


A-A' 剖立面（東西向・證明都市關係）

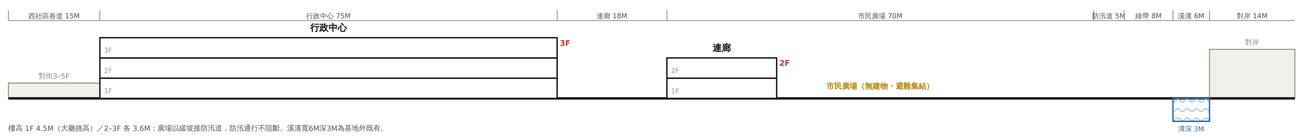


樓高 1F 4.5M（大廳挑高）／2–3F 各 3.6M；廣場以緩坡接防汛道，防汛通行不阻斷。溪溝寬6M深3M為基地外既有。

B-B' 剖立面（南北向・證明機能與高度）

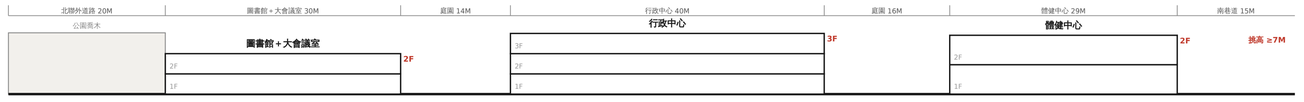

體健中心以 2 層達 4,000㎡：游泳池與籃球場需大跨距並挑高 ≥7M，非以總樓地板＋層數概算。

局部透視　市民廣場望向溪岸

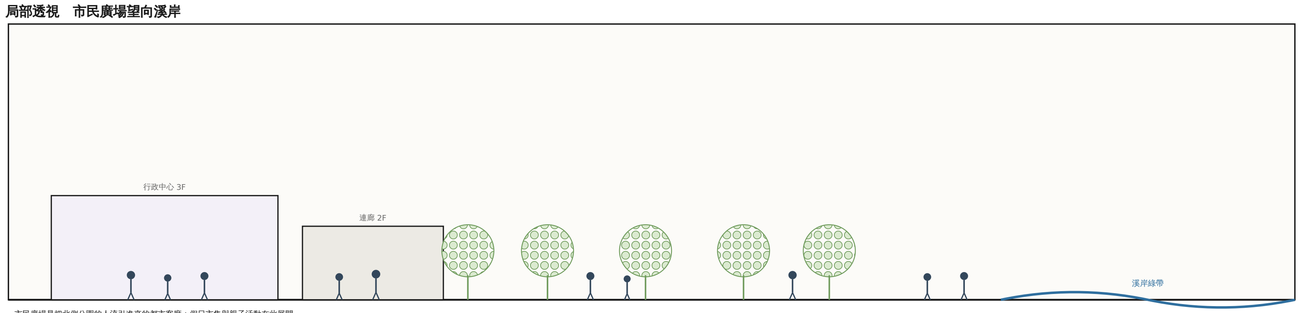

市民廣場是把北側公園的人流引進來的都市客廳：假日市集與親子活動在此展開，
東側緩坡接溪岸綠帶，長者散步、孩童戲水，行政洽公者也在此等候與停留。

溪園大客廳

某地方區政中心｜開放透明・服務 8 萬人口・都市大客廳


申論題（30 分）

列舉敷地計畫程序中的分析作業項目，並以你的
過去工作經驗，描述各項作業的資料取得方式或
來源；並可以經手過的工作為例，用圖文說明分析
如何引導出獨特且令人振奮的設計方向。

（一）分析作業項目與資料來源

自然	氣候・地形・地質土壤・水文・植生	氣象署／地調所／水利署淹水潛勢圖
人為	土地使用・交通・鄰棟天際線・噪音	現勘／都計圖／交通局流量
法規	分區・建蔽容積・退縮・建築線	都發局都計書圖／建管處
非量化	歷史・記憶・場所感	口述歷史／老地圖／田野訪談

（二）分析如何引導設計方向〔以本案示範〕

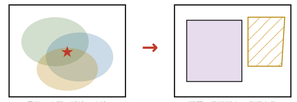

1. 水文與防汛分析發現：東側 5M 防汛道禁汽機車，
一般視為「不能用的邊」。
2. 人流分析發現：主要人流自北側 20M 路而來，
而北側隔路正是大型公園。
3. 疊圖洞見：把「不能行車的東邊」與「公園來的人流」

⚠ 原題設「可以」用經手案例，非強制。
無此經驗應明說為練習案例，不捏造親歷。

**小結：分析的價值不在項目齊全，而在從交疊處
讀出「只有這塊基地才有」的條件並放大。**

本年官方圖說要求｜逐項打勾

- **規劃設計構想**　左欄①–④＋中欄配置　✓
- **建築配置與地面層景觀**　中欄主圖 S=1:800　✓
- **剖立面圖**　A-A' 都市關係／B-B' 機能高度　✓
- **全區或局部透視圖**　市民廣場望向溪岸　✓

數值證據分級（本張圖）

題目給定　建蔽50%／容積200%／9,000・4,000・4,500㎡
地下汽90標50・地面自行車120・基地不淹水
圖推概算　A≒31,937.5㎡（近似梯形，北188/南177/深175）
自訂方案　量體分棟位置・大廳850㎡・開挖範圍・生態水池
未　指定　開挖率上限・建築高度上限 → 只標示不設限

**交卷前：圖名・比例尺・指北・剖面樓高數字、
透視有人物、每條算式數字與圖上一致、
題目點名條件逐條指得出位置。**

法規檢核｜法源→本案落點

法源（簡稱）	要求	本案落點
都計法 §22	細部計畫定土管、公設用地	依區政中心用地：建蔽50%／容積200%
通盤檢討辦法	都市設計應表明：地下室開挖限制	開挖退基線 12M 內緣，D/A=36.3%
技則 §162-1-3	法定停車空間得不計入容積	B1 停車 90 輛不計入 F
技則 §302	建築基地綠化量	溪岸綠帶＋廣場喬木，一樓留土植穴
技則 §305	基地保水	廣場透水鋪面＋生態水塘為保水設施
技則 §4-3	雨水貯集：基地面積×0.045 m³/㎡	31,937.5×0.045≈1,437 m³〔算式在此〕
技則 §39-1	日照：不使鄰地冬至日照<1hr	南側 15M 巷道側量體控 2F，退 14M
技則 §141	防空避難設備	B1 兼防空避難，出入口面市民廣場
水利法・出流管制	都計區 0.2 公頃以上	本案 3.19 公頃：滯洪＋排入東溪需申請

※ 條號僅供本課查核；考場圖上寫簡稱即可，不背條號。

課題→對策→效益（三行原則）

課題｜公園與溪流分屬兩側，基地成阻隔
對策｜東北象限退讓為市民廣場，形成公園—廣場—溪岸連續步道
效益｜外部資源轉為本案的到達動機

課題｜三量體尺度進大，臨 15M 巷道壓迫
對策｜行政 3F 置中、圖書與體健各 2F 分別南北，沿巷道 14M
效益｜街廓由高到低過渡，日照與風廊留通

課題｜東溪汛期水位高
對策｜首層 FL 抬 1.0M、B1 出入口反梯概，防汛道不阻斷
效益｜淹水不進地下、避難層可用

課題｜地方中心平日使用率低
對策｜廣場為無建物避難集結地，假日兼市集；圖書館獨立出入
效益｜一地多時段使用，管理可分區關閉

基地核對｜與官方底圖疊合


道路	北 20M／西・南 15M／東 5M 防汛道	✓ 未新增、未拓寬
公園	北側大型公園在基地外	✓ 位置未移、未占用
溪流	東側溪流＋6M 防汛道＋8M 綠帶	✓ 在基地外，不計入 A
凹口	東南角斜切（南 177M<北 188M）	✓ 保留斜邊，未填平
樹位	原題未標樹位	✓ 本案新植喬木，未移既有樹
界線	全部量體與開挖線在界內	✓ 開挖退界線 12M 以上

量體計算式（逐行可校核）

A = (188+177)/2 × 175 = 31,937.5 ㎡〔圖推概算・近似梯形〕
B上限 = A×50% = 15,968.75 ㎡　F上限 = A×200% = 63,875 ㎡
需求 G = 行政 9,000＋體健 4,000＋圖書及大會議 4,500 = 17,500 ㎡
G / F上限 = 17,500 / 63,875 = 27.4%〔容積用量低，故壓圖數換開放空間〕
投影 B = 圖書 2,250＋行政 3,000＋體健 2,000＋大廳連廊 876 ≒ 8,126 ㎡
建蔽率 = 8,126 / 31,937.5 = 25.4% ≦ 50% ✓　平均層數 ≒ 17,500/8,126 ≒ 2.15
開挖 D = 84M × 138M = 11,592 ㎡　開挖率 = 36.3%〔題目未上限，本案自訂〕
雨水貯集 = 31,937.5 × 0.045 ≒ 1,437 m³〔技則 §4-3〕

① 基地硬條件與環境


基地　L 形＝50 M × 59 M 外框扣 25 M × 14 M 凹口
A＝2,950−350＝2,600 ㎡〔圖推概算〕
分區　新開發都市・住商混合　建蔽 45%／容積 225%
西南　埤塘公園（假日遊客多）→ 英雄條件・主開放面
東北　國民小學徒門接送 → 避車彎、人車安全
基地內　既有樹木 → 中庭核心
全區　3 M 無遮簷人行道環基地〔題目給定〕
⚠ 圖示北向為斜向，不能把紙面上方直接當北。
⚠ 舊版誤以 50×59＝2,950 計（漏扣凹口），高估 13.46%。

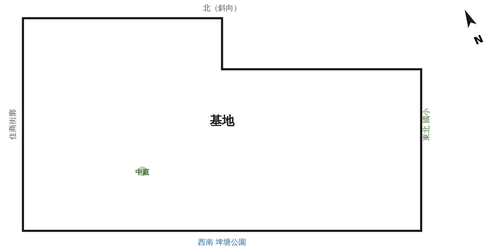

② 英雄條件・課題與對策

英雄條件：西南埤塘公園（假日人潮）

課題 1　基地小（2,600 ㎡）又是 L 形，易切得零碎
對策　量體沿北與東環抱，中間留完整中庭，不切小塊
課題 2　住宅要安靜、共享辦公要開放，兩者衝突
對策　公共交流在外（西南面埤塘）、安靜住辦在內（東北）
1F 共享交流對外，2F 以上住辦，門廳分設
課題 3　東北國小尖峰接送與本案車流交會
對策　地下車道設凹口側，接送避車彎留在道路上不進基地
課題 4　基地內既有樹易被地下室開挖犧牲
對策　開挖做 L 形，避開中庭樹木根域，樹下成為共享核心

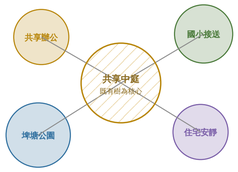


縮圖示意・不代表比例；正圖見中欄配置。

③ 空間需求・量體與開放空間

法規檢核（A/B/G/F/D 五帳）


項目	法定	本案	
基地 A	—	**2,600 ㎡**	—
建蔽率	45%	**41.2%**	✓
建築面積 B	≤1,170 ㎡	**1,072 ㎡**	✓
容積率	225%	**193.2%**	✓
計容積 F	≤5,850 ㎡	**5,024 ㎡**	✓
開挖率 D/A	未給上限	**42.7%**	—

住宅 套房 25×20＋一房 40×20＋二房 60×10＝1,900 ㎡（淨）
戶數 50 戶。比例 2:2:1〔題目給定〕；房型面積為自訂方案
含公設（口徑：公設占總面積 30%）＝1,900÷0.7≈2,714 ㎡
⚠ 不可與「淨面積 ×1.3＝2,470」混用——圖上須寫明採何口徑。
共享辦公＝300＋150＋100＋200＋200＋120＋200＋100＝1,370 ㎡
⚠ 舊版誤加為 1,570，多算 200 ㎡。

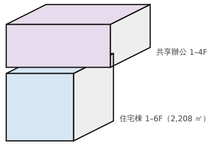


④ 人車動線・防災與管理

人行　主入口設西南面埤塘；3 M 無遮簷人行道環基地連續不中斷。
車行　地下車道出入口設凹口側，完全避開東北國小接送段。
接送　國小避車彎留在道路上，不引入基地內部。
停車　以地下為主（車位數題面未給，不捏造）；機車與自行車分設。
防災　中庭與西南平台為無建物避難集結地；B1 兼防空避難。
水文　中庭透水鋪面＋樹穴留土；雨水貯集供中庭澆灌。
管理　1F 共享交流可獨立開放，住宅門廳門禁獨立。
⚠ 高度與開挖率題目均未給統一上限，圖上明寫未指定。

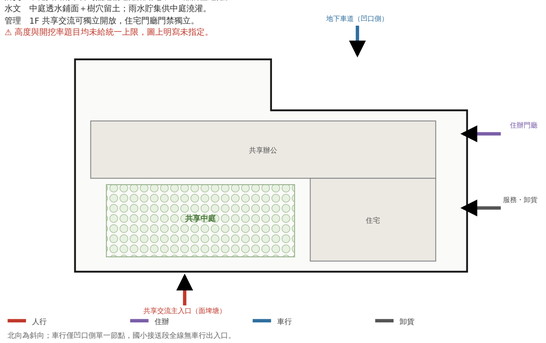

北向為斜向；車行僅凹口側單一節點，國小接送段全線無車行出入口。

111 年 敷地計畫與都市設計 80150｜考場版線稿（可校核）

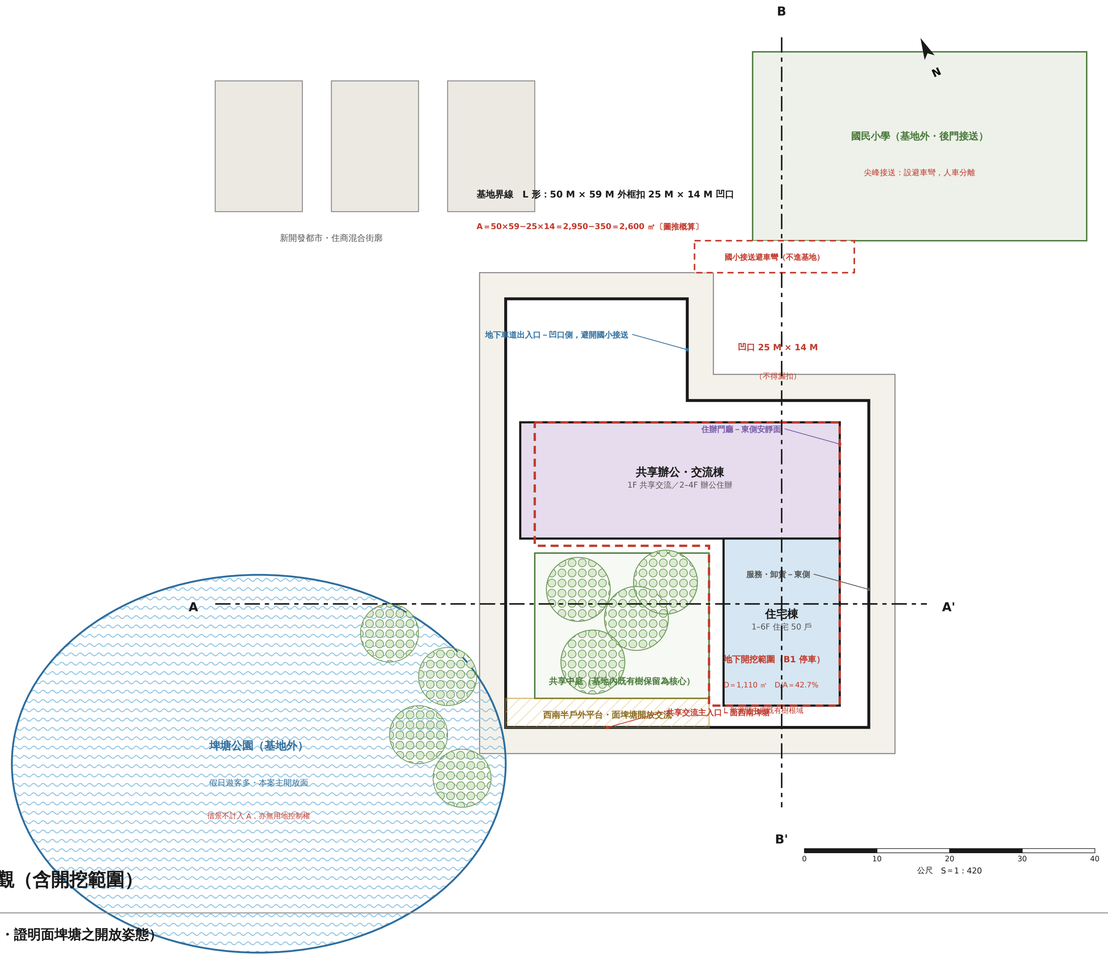


全區配置與地面層景觀（含開挖範圍）

A-A' 剖立面（西南—東北向・證明面埤塘之開放姿態）




1F 4.2M／2F 以上各 3.2M；西南向以半戶外平台與中庭層層遞退到埤塘，量體不臨水面壓迫。

B-B' 剖立面（證明凹口、車道與國小之關係）

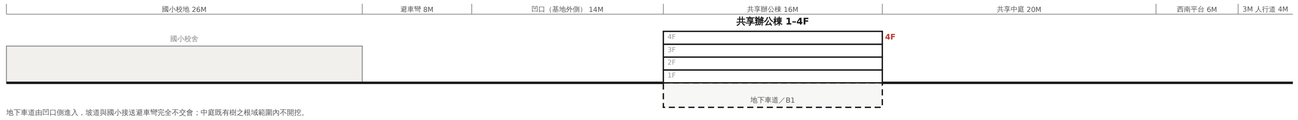

地下車道由凹口側進入，坡道與國小接送避車彎完全不交會；中庭既有樹之根域範圍內不開挖。

局部透視　西南半戶外平台望埤塘公園

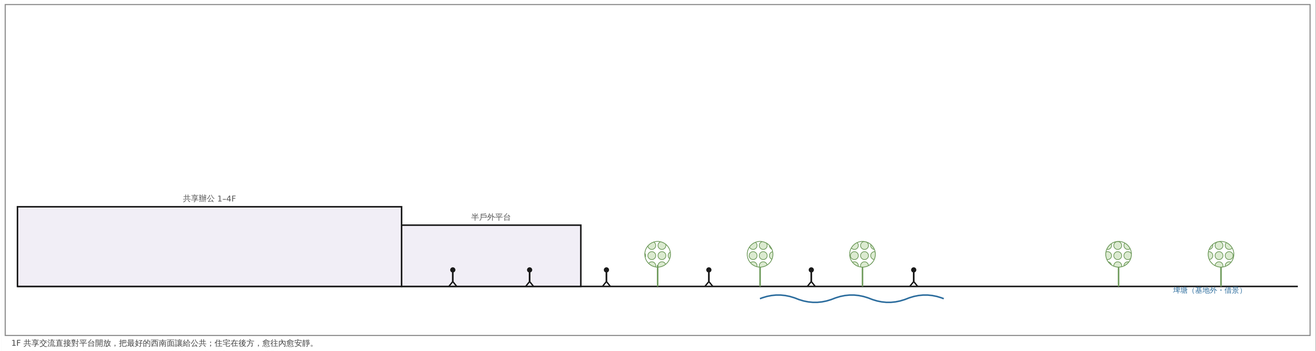

1F 共享交流直接對平台開放，把最好的西南面讓給公共；住宅在後方，愈往內愈安靜。
埤塘在基地之外——本案只借景與連接，不重成自家水域，也不計入法定空地。

共享聚落・埤塘客廳

複合型共享辦公基地｜住商混合 45%／225%｜量體環抱中庭・西南開向埤塘

申論題（30 分）

說明「韌性街道」的意涵，並以一條都市街道為例，
繪製其街道斷面並說明各項配置如何提升韌性。

（一）韌性街道的三個轉變

由車到人	路權重分配：縮車道、加人行 本案 3 M 無遮簷人行道環基地
由排到蓄	由快速排水轉為滯蓄入滲 側溝改草溝、透水鋪面
由單一到複合	平時通行、災時避難與供水 街道兼避難點線與集結

（二）示範街道斷面（自訂方案）

人行 4＋綠帶 2.5＋自行車 2.5＋車道 3×3.5 ＝ 一側 19.5 M
兩側對稱 19.5×2 ＝ 39 M，加中央分隔 4 M → 總寬 43 M。
各項：行道樹遮陰降溫、草溝滯蓄、路口縮寬縮短穿越距離。

⚠ **43 M 為本斷面之自訂方案，題目未指定總寬；**
不可寫成「約 40 M」含糊帶過。

（三）小結

韌性街道＝把道路從「車的通道」升級為藍綠基盤與人本廊道。
本案 3 M 人行道與埤塘藍綠基盤相接，即為此原則的基地版。

本年官方圖說要求｜逐項打勾

全區配置與量體 含 L 形基地凹口、3 M 人行道、開挖範圍	✓
機能關係圖 共享辦公／住宅／中庭之內外分層	✓
剖立面各 ≥1 A-A' 面埤塘開放姿態／B-B' 凹口與車道	✓
透視 ≥1 西南半戶外平台望埤塘，含人物	✓

數值證據分級（本張圖）
題目給定：45%／225%、住宅 50 戶與 2:2:1、3 M 無遮簷人行道
圖推概算：A＝50×59−25×14＝2,600 ㎡（L 形，依題圖量取）
自訂方案：房型面積、樓層、公設口徑、開挖範圍、街道斷面 43 M
題目未指定：車位數、高度上限、開挖率上限 → 圖上明寫未指定

交卷前：圖名・比例尺・指北・剖面樓高數字、
透視有人物、每條算式數字與圖上一致、
題目點名條件逐條指得出位置。

法規檢核｜法源→本案落點

法源（簡稱）	要求	本案落點
都計法 §22	細部計畫定土地使用分區管制	住商混合 45%／225%
通盤檢討辦法	都市設計應表明地下室開挖之限制	L 形開挖避開中庭樹，D/A＝42.7%
技則 §162-1-3	法定停車空間得不計入容積	B1 停車不計入 F
技則 §302	建築基地綠化量	中庭既有樹保留＋複層植栽
技則 §305	基地保水	中庭透水鋪面＋樹穴留土
技則 §4-3	雨水貯集：基地面積×0.045 m³/㎡	2,600×0.045＝117 m³
技則 §39-1	日照：住宅鄰地冬至日照<1hr	住宅棟退東界，量體控 6 層
樹木保護自治條例	受保護樹木原地保留	中庭既有樹依地方條例檢討

※ 條號僅供本庠查核；考場圖上寫簡稱即可，不背條號。

課題→對策→效益（三行原則）

課題｜L 形基地只有 2,600 ㎡，切碎就全毀
對策｜量體沿北與東環抱，中間留一個完整中庭，不做零碎小院
效益｜小基地也有一個像樣的公共核心

課題｜共享辦公要開放、住宅要安靜
對策｜公共交流在外（西南面埤塘）、安靜住辦在內（東北），門廳分設
效益｜兩種需求各得其所，不互相干擾

課題｜東北國小尖峰接送與本案車流交會
對策｜地下車道改設凹口側，接送避車彎留在道路上不進基地
效益｜學童動線與車流完全不交會

課題｜中庭既有樹易在開挖時消失
對策｜開挖做 L 形，避開樹木根域；樹下成為共享中庭核心
效益｜樹蔭降暑變成本案最有價值的既有資產

基地核對｜與官方底圖疊合

凹口	25 M × 14 M，不得漏扣	✓ 保留凹口，A 已扣除
埤塘	西南側，基地外	✓ 借景不計入 A，未占用
國小	東北側，基地外	✓ 該側不設車行出入口
樹木	基地內既有樹	✓ 原地保留為中庭核心
人行道	3 M 無遮簷，環基地	✓ 連續不中斷，題目給定
北向	題圖為斜向	✓ 指北針依題圖斜置，未擅自轉正


量體計算式（逐行可校核）
A ＝ 50×59 − 25×14 ＝ 2,950 − 350 ＝ 2,600 ㎡〔圖推概算〕
B上限 ＝ A×45% ＝ 1,170 ㎡　F上限 ＝ A×225% ＝ 5,850 ㎡
住宅淨 ＝ 25×20＋40×20＋60×10 ＝ 500＋800＋600 ＝ 1,900 ㎡（50 戶，2:2:1）
住宅含公設 ＝ 1,900 ÷ 0.7 ≈ 2,714 ㎡（口徑：公設占總面積 30%）
共享辦公 ＝ 300＋150＋100＋200＋200＋120＋200＋100 ＝ 1,370 ㎡〔題目加總〕
投影 B ＝ 辦公棟 704＋住宅棟 368 ＝ 1,072 ㎡　建蔽 ＝ 41.2% ≦ 45% ✓
G ＝ 704×4F＋368×6F ＝ 2,816＋2,208 ＝ 5,024 ㎡　容積率 ＝ 193.2% ≦ 225% ✓
開挖 D ＝ 42×17＋18×22 ＝ 714＋396 ＝ 1,110 ㎡　開挖率 ＝ 42.7%〔未給上限〕
雨水貯集 ＝ 2,600 × 0.045 ＝ 117 m³（技則 §4-3）

111 年 複合型共享辦公基地｜80150 敷地計畫與都市設計｜考場復原稿（可校核線稿）

① 基地硬條件與環境

基地　矩形 120 M × 70 M＝8,400 ㎡〔題目給定〕
分區　商業及住宅區　建蔽 55%／容積 360%〔題目平均約值〕
西　30 M 道路＋上方高架（約 10 M 高・噪音震動明顯）
北　15 M 道路；對側住宅 7–9 層＋鄰里公園（基地外）
南　20 M 道路（次入口）　東　10 M 道路（安靜側）
基地內　歷史水圳斜向穿越（地面下「可能」仍保有遺址）
基地內　東北角既有樹群

△ 55%／360% 為題目提供之平均約值，非各分區法定率。
⚠ 水圳為疑似遺址，非法定禁挖區；避讓帶寬為自訂方案。

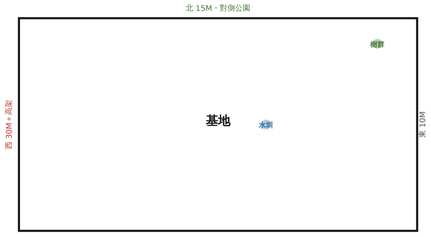

② 英雄條件・課題與對策

英雄條件：歷史水圳斜穿＋西側高架干擾

課題 1　水圳穿越使基地被切開、地下有疑似遺址
對策　化為線性開放軸：地面再現、優先避挖，量體分立兩側
課題 2　西側高架噪音震動、量體大不易分割
對策　高架側設隔音牆＋複層密植＋服務停車緩衝帶
安靜機能（住宿、圖書）遠離高架，置東側
課題 3　容積 360% 量大，恐擠壓公益開放感
對策　本案僅用 6,480 ㎡（21.4%），以留空換公共性
課題 4　東北角既有樹群易被施工破壞
對策　樹群原地保留，結合庭園與兒童遊戲場，開挖避開


縮圖示意・不代表比例；正圖見中欄配置。

③ 空間需求・量體與開放空間

法規檢核（A/B/G/F/D 五帳）


項目	法定	本案	
基地 A	—	**8,400 ㎡**	—
建蔽率	55%	**33.3%**	✓
建築面積 B	≤4,620 ㎡	**2,800 ㎡**	✓
容積率	360%	**77.1%**	✓
計容積 F	≤30,240 ㎡	**6,480 ㎡**	✓
開挖率 D/A	未給上限	**31.8%**	—

題目機能加總　5,300 ㎡〔題目給定項目淨面積〕
本案方案總量　6,480 ㎡〔方案：含公設與動線〕
研修教學 1,760 ㎡／住宿研習 2,640 ㎡／公益展演圖書 2,080 ㎡
⚠ 6,500 ㎡ 是方案假設，不得當題目給定值。
停車 汽 30＋機 20〔題目給定〕，全置 B1 水圳西側。

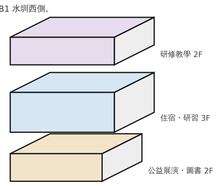


④ 人車動線・防災與管理

人行　北側對鄰里公園設穿越，南側 20 M 設次入口。
車行　西側緩衝帶進出，避開高架匝道與北側人流。
卸貨　西側緩衝帶內設避車，不進入公益廣場。
停車　地下 B1 汽 30／機 20〔題目給定〕；開挖止於水圳避讓帶。
防災　公益廣場為無建物避難集結地；B1 兼防空避難。
水文　沿圳設草溝與雨花園，透水鋪面；出流經滯蓄後排放。
振動　僅靠擋牆與服務帶不足以隔絕地傳振動，須另作結構隔振或距離評估〔本案標為待評估〕。
管理　公益展演獨立出入口，假日可單獨開放。

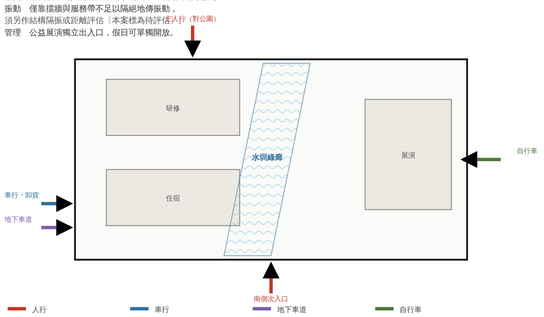


人車分道：車行只走西側緩衝帶；水圳綠廊全線步行，災時為避難動線。

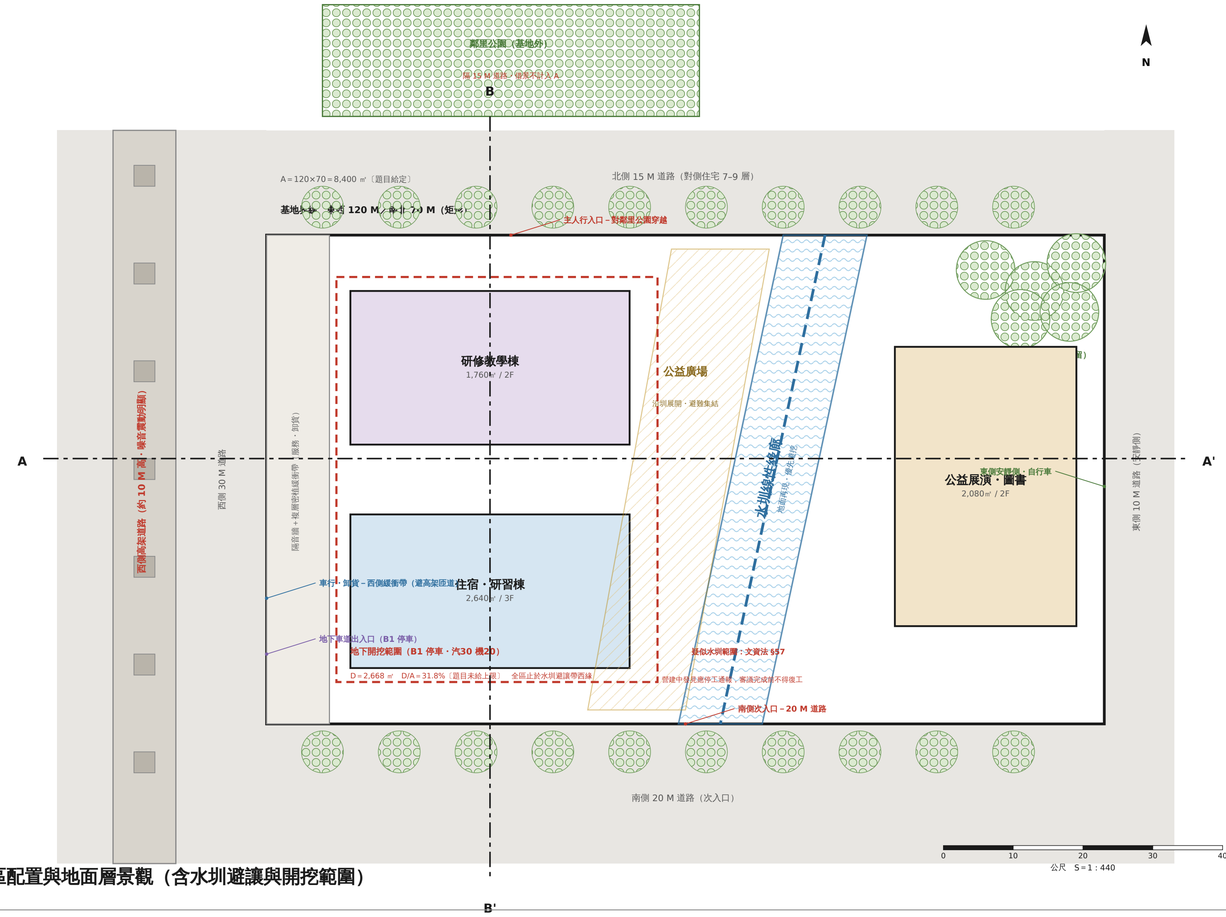


全區配置與地面層景觀（含水圳避讓與開挖範圍）

A-A' 剖立面（東西向・證明高架緩衝與水圳關係）

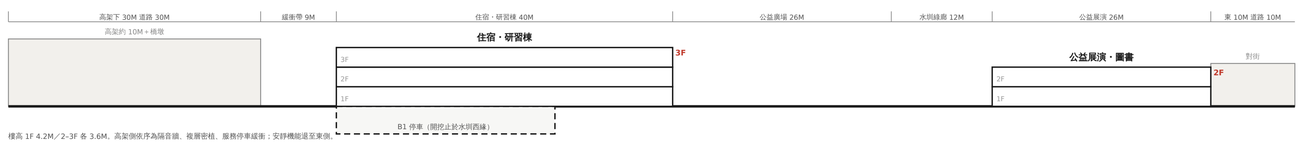


樓高 1F 4.2M／2–3F 各 3.6M。高架側依序為隔音牆、複層密植、服務停車緩衝；安靜機能退至東側。

B-B' 剖立面（南北向・證明機能與高度）

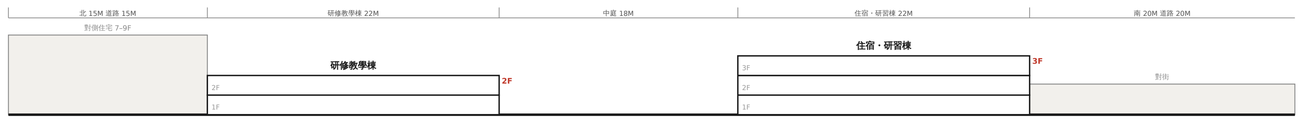

量體 2–3 層，低於對側住宅 7–9 層，天際線由北向南遞降；中庭南向採光、兼通風廊道。

局部透視　水圳綠廊由南望北

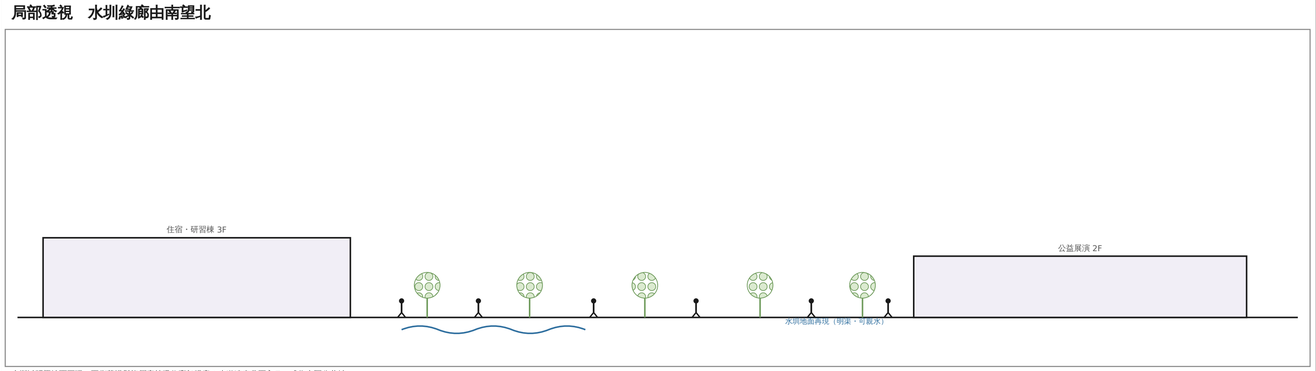

水圳以明渠地面再現，兩側草溝與複層密植吸收高架噪音；步道連南北兩入口，成為全區公共軸。
沿圳設座椅與解說，說明此處為疑似水圳範圍、地下優先避挖——把法規限制畫成公共空間的理由。

水圳再生・公益綠廊

公益教育研修中心｜商業及住宅區 55%／360%｜水圳穿越・西臨高架

申論題（30 分）

說明敷地計畫中「非量化基地分析」的意義，並以本案為例，說明哪些非量化資訊影響配置決策，如何取得，以及如何在圖面上被讀出來。

（一）非量化資訊的三個來源

現場	感官與行為：噪音、震動、氣味、日照 高架下實地停留、不同時段記錄
文獻	地籍圖、舊航照、水利圖、口述 水圳走向與舊河道事舊圖比對
法制	疑似遺址、文資通報、都審意見 文資法 §57、地方都審紀錄

（二）本案三項決定性的非量化資訊

1. 水圳是「記憶的線」，而非只是障礙 → 由避讓轉為公共軸。
2. 高架的干擾是連續的、方向性的 → 用帶狀緩衝而非點狀屏障。
3. 東北樹群是既有的社會場所 → 保留比新植更有價值。

⚠ 題目說地下「可能」仍保有遺址＝疑似，
非法定禁挖區；寫「優先避挖，調查確認後調整」。

（三）小結

量化資訊決定「能放多少」，非量化資訊決定「該放哪裡」。
本案容積只用 21.4%，正是非量化判斷壓過量體最大化的結果。

本年官方圖說要求｜逐項打勾

規劃理念與全區配置 含水圳再應、開挖範圍、人車動線、防救災	✓
機能關係圖 研修／住宿／公益展演三群與水圳軸之關係	✓
剖立面各 ≥1 A-A' 東西向（高架緩衝）／B-B' 南北向（高度）	✓
透視 ≥1 水圳綠廊由南望北，含人物與尺度	✓

數值證據分級（本張圖）
題目給定：120×70＝8,400 ㎡、55%／360%（平均約值）、停車汽30機20
圖推概算：水圳走向由題圖虛線量取，(80,0)→(65,70)
自訂方案：避讓半寬 6 M、量體分區、樓層、開挖範圍、6,480 ㎡ 總量
題目未指定：高度上限、開挖率上限、綠覆率 → 圖上明寫未指定

交卷前：圖名・比例尺・指北・剖面樓高數字、
透視有人物、每條算式數字與圖上一致、
題目點名條件逐條指得出位置。

法規檢核｜法源→本案落點

法源（簡稱）	要求	本案落點
文資法 §57	發見疑似遺址應通報；施工中停工	水圳帶優先避挖，圖上註停工通報程序
都計法 §22	細部計畫定土地使用分區管制	商業及住宅區 55%／360%（題目值）
通盤檢討辦法	都市設計應表明地下室開挖之限制	開挖止於水圳避讓帶西緣，D/A＝31.8%
技則 §162-1-3	法定停車空間得不計入容積	B1 汽30 機20 不計入 F
技則 §302	建築基地綠化量	沿圳複層密植＋東北樹群保留
技則 §305	基地保水	透水鋪面＋草溝＋雨花園
技則 §4-3	雨水貯集：基地面積×0.045 m³/㎡	8,400×0.045＝378 m³
噪音管制法	交通噪音防制	隔音牆＋複層密植＋緩衝量體（振動另評估）

※ 條號僅供本庫查核；考場圖上寫簡稱即可，不背條號。

課題→對策→效益（三行原則）

課題｜水圳斜穿把基地切成兩半
對策｜不視為障礙，改為線性開放軸；量體分立東西兩側，地下開挖止於西緣
效益｜限制變成全區唯一的公共軸線

課題｜西側高架噪音與震動連續且有方向性
對策｜帶狀緩衝：隔音牆＋複層密植＋服務停車；安靜機能全部退到東側
效益｜干擾在進入建築前已被三層削減

課題｜容積 360% 量大，恐把公益感擠掉
對策｜只用 21.4% 容積、建蔽 33.3%，其餘還給廣場與綠廊
效益｜公益性用留空證明，不是用標語

課題｜東北樹群易在施工期損失
對策｜樹群原地保留為庭園與兒童遊戲場，開挖線退開，設施工圍籬範圍
效益｜既有社會場所延續，綠覆不必從零長起


基地核對｜與官方底圖疊合

道路	西 30M／北 15M／南 20M／東 10M	✓ 未新增、未拓寬
高架	西側道路上方，約 10 M 高	✓ 位置未移，畫出橋墩
水圳	斜向穿越，題圖為虛線	✓ 走向未改，僅加註避讓帶
樹群	東北角基地內既有樹木群	✓ 原地保留，未移植
公園	北側鄰里公園在基地外	✓ 隔 15M 道路，不計入 A
界線	矩形 120×70，無凹口	✓ 量體與開挖均在界內

量體計算式（逐行可校核）
A = 120 × 70 = 8,400 ㎡〔題目給定〕
B上限 = A×55% = 4,620 ㎡　F上限 = A×360% = 30,240 ㎡〔題目平均約值〕
題目機能加總 = 5,300 ㎡〔題目給定項目淨面積〕
投影B = 研修 880＋住宿 880＋展演 1,040 = 2,800 ㎡　建蔽 = 33.3% ≦ 55% ✓
G = 880×2＋880×3＋1,040×2 = 6,480 ㎡　容積率 = 77.1% ≦ 360% ✓
F 用量 = 6,480 / 30,240 = 21.4%（刻意不用滿，換取沿圳留空）
開挖 D = 46M × 58M = 2,668 ㎡　開挖率 = 31.8%〔題目未給上限〕
雨水貯集 = 8,400 × 0.045 = 378 m³（找到 §4-3）

① 基地硬條件與環境

基地　70 M × 50 M＝3,500 ㎡〔題目給定〕東北轉角截角未標尺寸
分區　市場用地（公共設施用地）　建蔽 45%／容積 300%
北　30 M 道路；對側商業 12 層、1 樓餐廳 → 主人流
南　15 M 道路；對側宗教區廟宇坐北朝南
基地面對的是廟宇「北側」樹群與休憩庭園（非廟埕）
東　20 M 道路（對側住宅）→ 社宅較安靜面
西　國民小學（後門接送）→ 人車安全第一
△ 既有樹群在道路對側、基地外，不得當基地內保留樹或法定綠地。
⚠ 出流管制 0.2 公頃門檻為 114 年 9 月新制，非 113 年當時法規。

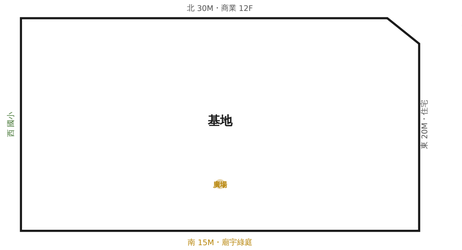

② 英雄條件・課題與對策

英雄條件：公設用地要疊住宅＋南側廟宇綠庭

課題 1　市場用地不能直接蓋社宅
對策　依多目標使用辦法循「公共使用／社會福利設施」途徑
市場置 1F、2F，社宅自 3F 起，維持市場原有服務機能
課題 2　公（市集）私（住宅）混雜、安全與尊嚴
對策　垂直分層＋東側獨立門廳電梯門禁，動線完全分離
課題 3　南面對廟宇北側綠庭，量體易壓迫
對策　南側 17 M 退為廣場，低層退讓、借景綠庭不占用
課題 4　西側國小接送與市集人車衝突
對策　車道移至東側 20 M 道路，北側卸貨與人流錯開時段




縮圖示意，不代表比例；正圖見中欄配置。

③ 空間需求・量體與開放空間

法規檢核（A/B/G/F/D 五帳）


項目	法定	本案	
基地 A	—	**3,500 ㎡**	—
建蔽率	45%	**42.9%**	✓
建築面積 B	≤1,575 ㎡	**1,500 ㎡**	✓
容積率	300%	**297.1%**	✓
計容積 F	≤10,500 ㎡	**10,400 ㎡**	△
開挖率 D/A	未給上限	**53.1%**	—

社宅 90 戶×40 ㎡＋60 戶×60 ㎡＝7,200 ㎡（淨）〔戶數為題目建議〕
公設以 ×1.25 計＝9,000 ㎡〔自訂方案〕；非住宅 1,400 ㎡
⚠ 只餘 100 ㎡，不到 1% 彈性——非住宅若增至 2,000 ㎡ 即逾 11,000 超限。
△ 若公設改以「占總面積 25%」＝7,200÷0.75＝9,600 ㎡，亦超限。
兩種口徑不可混用，圖上須寫明採何者。

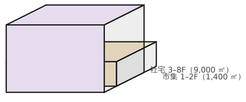


④ 人車動線・防災與管理

人行　北側 30 M 主人流進市集；南側廣場對廟宇綠庭設穿越。
車行　地下車道設東側 20 M 道路，完全避開西側國小接送。
卸貨　生鮮卸貨在北側西端，與市集主入口錯開、限時段。
停車　地下汽車（含無障礙）依技則按用途與樓地板核算，
方案：汽 75＋無障礙 3＋機 150〔方案・須依核定主管核算〕。
防災　廣場為無建物避難集結地；B1 兼防空避難；社宅二方向避難。
減洪　廣場透水鋪面＋地下滯蓄槽，滯蓄後再放流。
⚠ 有人、有車區域不得臨時受淹。
管理　市集與社宅分時段、分門禁；快閃攤位以 3×3 M 模矩彈性配置。

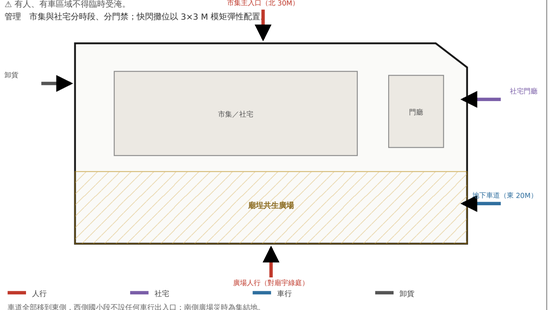

車道全部移到東側，西側國小段不設任何車行出入口；南側廣場英時為集結地。

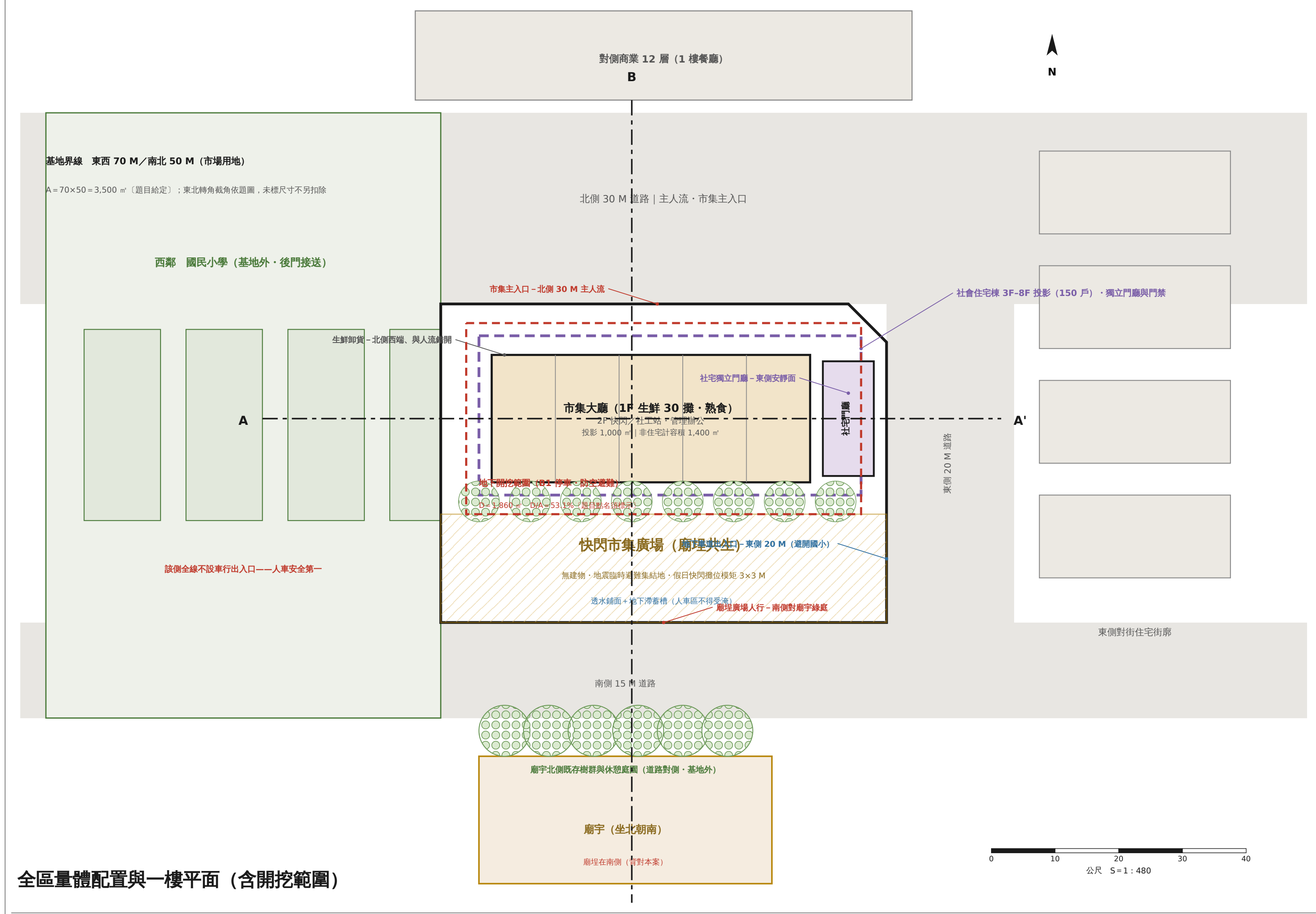


全區量體配置與一樓平面（含開挖範圍）

A-A' 剖立面（東西向・證明公私分層與門禁分離）




1F 4.5M（市集挑高）／2F 4.0M／3–8F 各 3.2M；社宅門廳自地面直上 3F，與市集完全不共用。

B-B' 剖立面（南北向・證明對廟宇之退讓與高度）

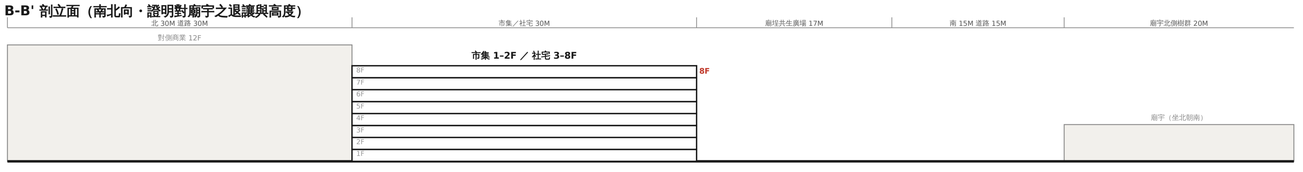

南側退 17 M 為廣場，社宅最高 8 層低於北側商業 12 層；向南遮陽，不壓迫廟宇北側樹群與休憩庭園。

局部透視　廟埕共生廣場由南望北（快閃市集日）

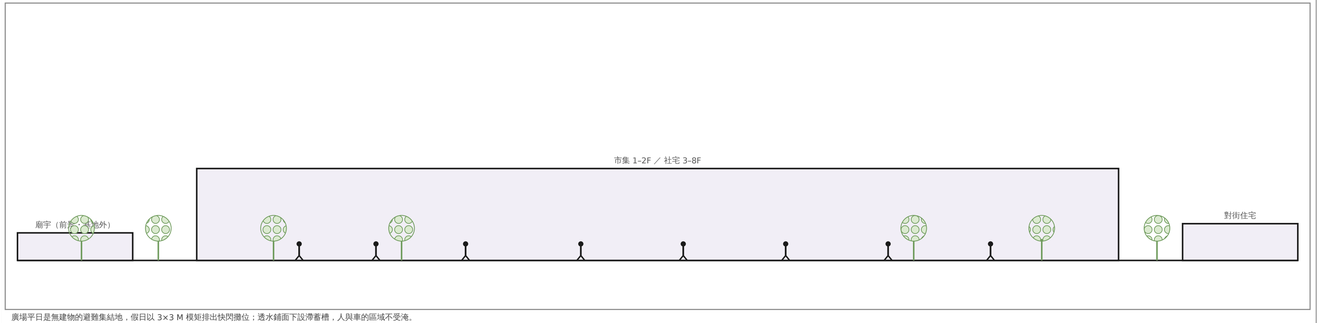

廣場平日是無建物的避難集結地，假日以 3×3 M 模矩排出快閃攤位；透水鋪面下設滯蓄槽，人與車的區域不受淹。
南望可見廟宇北側樹群與休憩庭園——借景而不占用；市集低層開放、社宅自 3F 起，門禁與尊嚴同時成立。

市集疊聚落・廟埕共生

快閃市集暨社會住宅｜市場用地 45%／300%｜公私垂直分層・南面廟宇綠庭

申論題（30 分）

說明都市水患成因，並分別從都市計畫、都市設計與敷地計畫三個層面，說明可行之減洪對策；並以本案說明敷地計畫層面的具體作為。

（一）三個層面的減洪對策

都市計畫	總量與區位：不透水面總量管制 劃設滯洪用地、保留行水區
都市設計	街廓尺度：藍綠基盤連續 退縮帶設草溝、廣場兼滯洪
敷地計畫	基地尺度：把基地變海綿 透水鋪面、雨花園、滯蓄槽

（二）本案敷地層面的具體作為

1. 廣場透水鋪面＋地下滯蓄槽，滯蓄後再放流，不直接排入公共溝。
2. 一樓市集地坪抬高並設防水閘；地下車道口設反樓檻與截水溝。
3. 屋頂綠化與雨水回收供沖廁澆灌；基地內逐流分流。

⚠ **滯洪有效容積須以設計水位差與出流設施驗證，**
生態池水面面積不能當有效容積。
⚠ **停車與市集區不得作為臨時受淹空間。**

（三）小結

減洪不是加一座池子，而是讓每一寸鋪面、每一道邊溝都參與。
本案以「廣場兼滯洪、平災兩用」把防災畫成日常的公共空間。

本年官方圖說要求｜逐項打勾

全區量體配置含一樓平面 市集攤位模矩、卸貨、門廳位置皆在圖上	✓
開挖範圍 D＝1,860 ㎡、D/A＝53.1%，紅虛線標示	✓
機能關係圖 市集／社宅／社工站與廣場之垂直分層關係	✓
剖立面各 ≥1、透視 ≥1 A-A' 分層門禁／B-B' 對廟退讓／廣場透視	✓

數值證據分級（本張圖）
題目給定：70×50＝3,500 ㎡、45%／300%、社宅 90／60 戶（建議）
圖推概算：東北轉角截角（題圖有、未標尺寸，不另扣除）
自訂方案：房型 40／60 ㎡、公設 ×1.25、樓層分配、停車數、開挖範圍
題目未指定：高度上限、開挖率上限、停車位數 → 圖上明寫未指定

交卷前：圖名・比例尺・指北・剖面樣高數字、
透視有人物、每條算式數字與圖上一致、
題目點名條件逐條指得出位置。

法規檢核｜法源→本案落點

法源（簡稱）	要求	本案落點
多目標使用辦法	公設用地得立體多目標使用	備公共使用／社福設施途徑，仍須個案核准
同辦法 §2	不得影響原公共設施機能	市場機能保留於 1F、2F，攤位數不減
同辦法 §2-1	新建後退流不超過興建前	廣場滯蓄槽與立柚核，不因公益性免除
住宅法	社會住宅只租不售、保障弱勢比例	150 戶只租不售，含無障礙住宅單元
技則 §59	停車空間依用途與樓地板核算	B1 汽 75＋無障礙 3＋機 150〔方案〕
技則 §141	防空避難設備	B1 兼防空避難，出入口面南側廣場
技則 §305	基地保水	廣場透水鋪面＋雨花園
水利法・出流管制	滯蓄後再放流	⚠ 0.2 公頃門檻為 114 新制，非 113 當時

※ 條號僅供本庫查核；考場圖上寫簡稱即可，不背條號。

課題→對策→效益（三行原則）

課題｜市場用地單疊入社會住宅，法源不足即違法
對策｜循多目標使用辦法之公共使用／社福設施途徑，市場置 1F、2F，社宅自 3F 起
效益｜用途、樓層與出入口都站得住，非只寫「多目標」三字

課題｜公私機能混雜，住戶尊嚴與安全受損
對策｜東側設獨立門廳、電梯與門禁，自地面直上 3F，與市集完全不共用
效益｜市集愈熱鬧，住宅愈安靜——兩者互不折損

課題｜南面對廟宇北側樹群，量體易壓迫
對策｜南側退 17 M 為廣場，低層退讓、向南遮陽；借景綠庭但不占用對側土地
效益｜廟與市集共生，公共空間有了對景

課題｜容積只餘 100 ㎡，方案毫無彈性
對策｜圖上直接判斷敏感度：非住宅增至 2,000 ㎡ 即超限；公設口徑改算亦超限
效益｜把風險說出來，比假裝剛好蓋得下更專業


基地核對｜與官方底圖疊合

道路	北 30M／南 15M／東 20M	✓ 未新增、未拓寬
國小	西側緊鄰，基地外	✓ 位置未移，該側不設車行口
廟宇	南側道路對側，坐北朝南	✓ 面對其北側樹群，未畫成廟埕
樹群	在道路對側、基地外	✓ 借景不計入綠地，未移植
截角	東北轉角，題圖未標尺寸	✓ 保留截角，A 仍採 3,500
界線	量體與開挖均在界內	✓ 南側退 17M 為廣場

量體計算式（逐行可校核）
A ＝ 70 × 50 ＝ 3,500 ㎡〔題目給定〕
B上限 ＝ A×45% ＝ 1,575 ㎡　F上限 ＝ A×300% ＝ 10,500 ㎡
社宅淨 ＝ 90×40＋60×60 ＝ 3,600＋3,600 ＝ 7,200 ㎡〔戶數為題目建議・房型自訂〕
社宅含公設 ＝ 7,200 × 1.25 ＝ 9,000 ㎡〔自訂口徑，圖上明寫〕
非住宅〔市場 1F 1,000＋2F 400〕＝ 1,400 ㎡
F ＝ 9,000＋1,400 ＝ 10,400 ㎡ ≦ 10,500 ✓（僅餘 100 ㎡，不到 1%）
投影 B ＝ 社宅棟 60×25 ＝ 1,500 ㎡　建蔽 ＝ 42.9% ≦ 45% ✓
開挖 D ＝ 62M × 30M ＝ 1,860 ㎡　開挖率 ＝ 53.1%〔題目點名須標〕
雨水貯集 ＝ 3,500 × 0.045 ＝ 157.5 m³（技則 §4-3）

① 基地硬條件與環境


基地　北寬 50 M（深 54 M）＋南窄 32 M（深 28 M），總深 82 M
A＝50×54＋32×28＝3,596 ㎡〔圖示量取〕／正文約 3,600 ㎡
分區　停車場用地　建蔽 80%／容積 400%
西　12 M 道路（2＋6＋4）；隔路為 33 M 園道
園道中央 14 M 生態排水渠（水位低道路約 2 M）
南　20 M 道路（2.5＋15＋2.5）　北　7 M 道路（對側 3–4 層）
東　商業區老舊 3–5 層街屋，緊臨道路設騎樓
都審　西側與南側「均」沿境界線退縮 4 M 無遮蓋帶狀開放空間
⚠ 正文 3,600 與圖示 3,596 不得混用分母；本張全案以 3,596 計。
⚠ 西側與園道之間隔 12 M 道路，不得逕自連向家綠地。

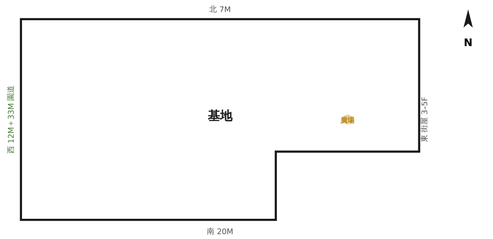

② 英雄條件・課題與對策

英雄條件：西側 33 M 園道與 14 M 生態排水渠

課題 1　停車量最大化會吃掉地面與高度
對策　停車立體收納於 6F 棟，取最大值 7–8 成；
省下的地面全部變成廣場、市集與運動——並在園上交代
課題 2　與園道隔 12 M 道路，看得到走不到
對策　設小橋／石階跨排水渠，連成題目要求之「部分連接」。
課題 3　六層≠可任意用六個 3 M 樓層
對策　羽球淨高 6.1 M＋結構設備，運動另立 5F 棟；
停車棟控在 6F／18 M，剖面標明兩者高度關係
課題 4　東側緊臨老舊街屋，北側 7 M 道路易回堵
對策　東側留 3 M 防火間隔＋灰善後巷；北側設等待區與機車專用道

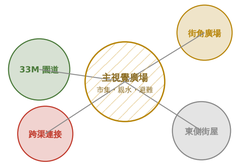


縮圖示意・不代表比例；正圖見中欄配置。

③ 空間需求・量體與開放空間

法規檢核（A/B/G/F/D 五帳）


項目	法定	本案	
基地 A	—	**3,596 ㎡**	—
建蔽率	80%	**49.2%**	✓
建築面積 B	≤2,876.8 ㎡	**1,771 ㎡**	✓
容積率	400%	**122.4%**	✓
多目標 F	≤1/3＝4,794.7	**4,400 ㎡**	✓
開挖率 D/A	未給上限	**45.7%**	—

運動需求 300+200+≥500+300 坪＝≥1,300 坪＝4,297.5 ㎡〔題目給定〕
⚠ 停車免計容積 ≠ 容積可全給運動：多目標容積一般 ≤ 總容積 1/3。
本案 4,400 ㎡ 落在 4,297.5 ～ 4,794.7 之間，餘裕僅 102.5 ㎡。
⚠ 社福用途經審議得放寬至 1/2，不能移用到運動設施。
餐飲另涉至少技則標準二倍之停車檢核。

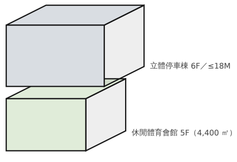


④ 人車動線・防災與管理

車行　汽車主出入口設北側 7 M 道路〔經交通檢核後採用，非理所當然〕。
設汽車等待區與機車專用道，不使車流回走街角廣場。
人行　運動主入口面西側主視覺廣場；南側沿 4 M 退縮帶進出。
連接　小橋／石階跨 14 M 排水渠與園道部分連接（題目點名）。
停車　地上 6F＋B1，約 155 輛〔方案・刻意不衝滿〕；機車位＝汽車位並分流。
防災　街角廣場與主視覺廣場為無建物避難集結地；B1 兼防空避難。
滯洪　⚠ 停車場兼滯洪不得使有人或有車區域臨時受淹；
本案改設獨立滯蓄槽，並交代緊急斷電、安全路徑與復原管理。
管理　西側 12 M 道路假日可設減速帶或封街為徒步街〔方案〕。

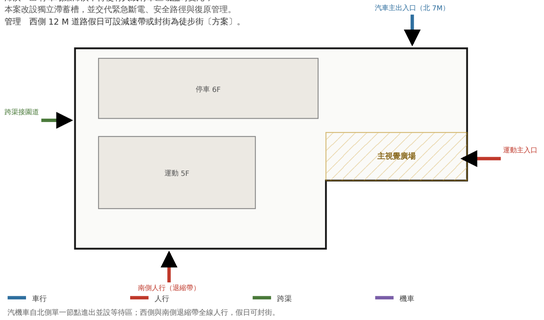


汽機車自北側單一節點進出並設等待區；西側與南側退縮帶全線人行，假日可封街。

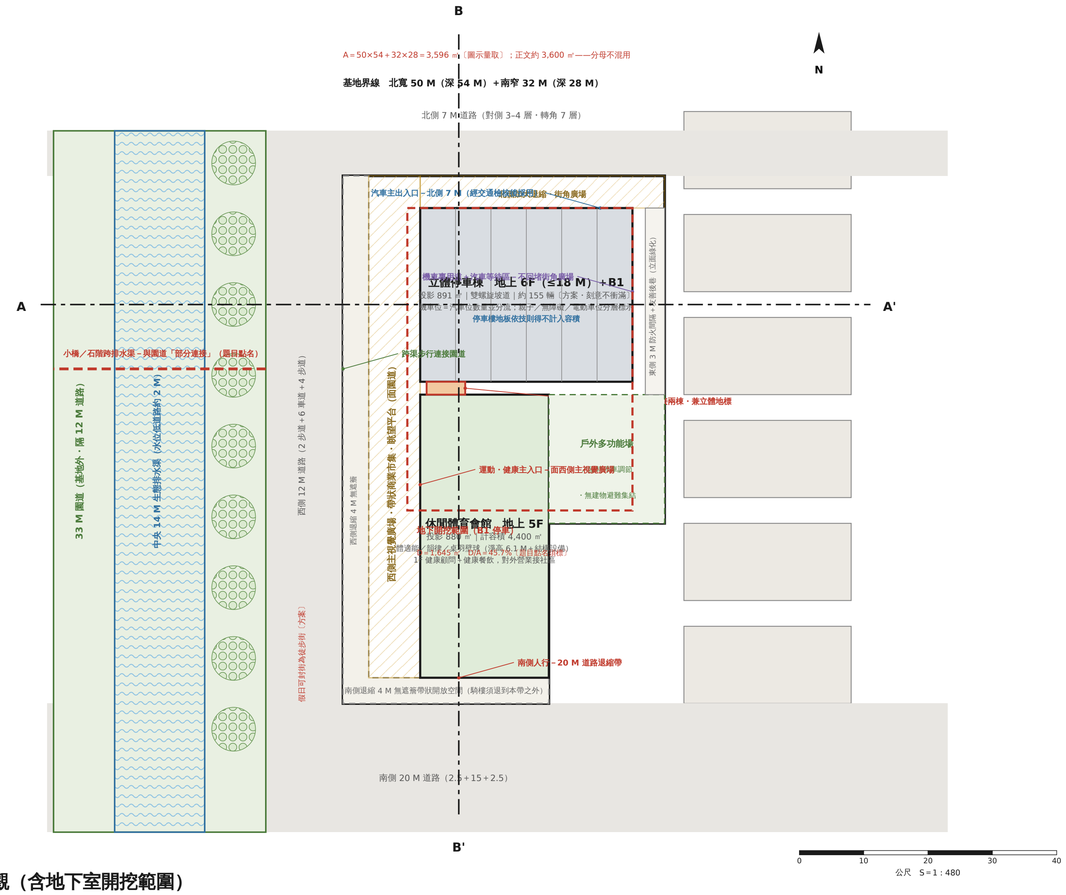


全區配置與地面層景觀（含地下室開挖範圍）

A-A' 剖立面（東西向・證明園道關係與控高）

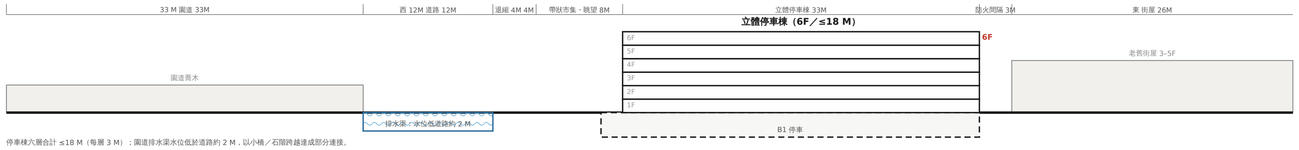


停車棟六層合計 ≤18 M（每層 3 M）；園道排水渠水位低於道路約 2 M，以小橋／石階跨越達成部分連接。

B-B' 剖立面（南北向・證明運動淨高與天際線）

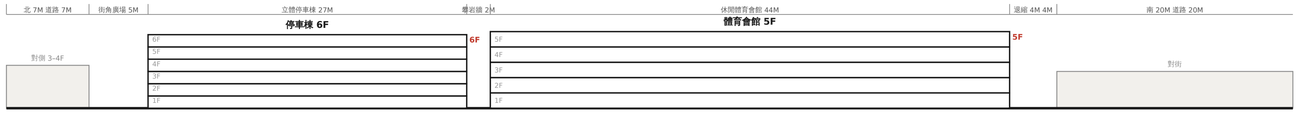

停車 3 M／層共 6 層；體育會館球場層淨高 6.1 M＋結構設備，故 5 層即接近 18 M——六層不等於六個 3 M 樓層。

局部透視　西側主視覺廣場望園道（親水平台與帶狀市集）

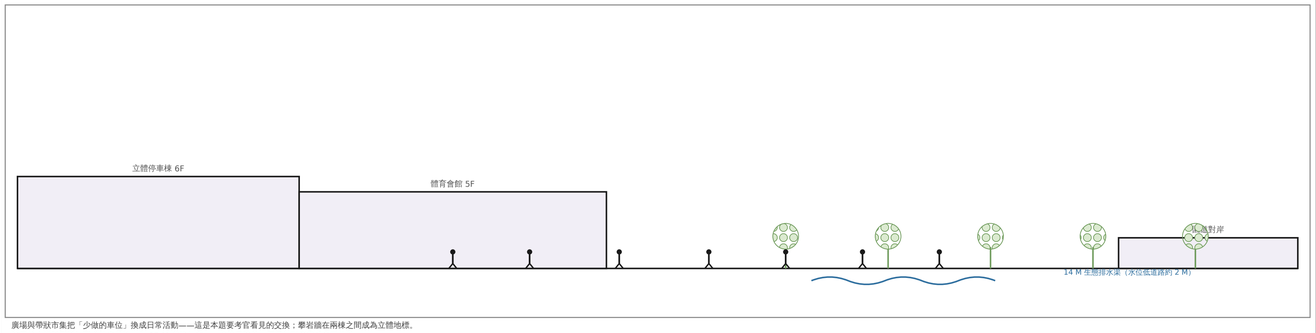

廣場與帶狀市集把「少做的車位」換成日常活動——這是本題要考官看見的交換：攀岩牆在兩棟之間成為立體地標。
跨渠的小橋與石階把園道拉進基地，但 12 M 道路仍在——連接是跨越，不是把對岸畫成自家綠地。

園道之丘

停車場立體多目標使用複合休閒運動設施｜停車場用地 80%／400%｜面園道・控高 6F/18M

申論題（30 分）

以 Kevin Lynch 都市意象五元素為前導，說明面對氣候
變遷與都市老化，都市空間「立體化」可採行的韌性
作為，並分六類具體說明。

（一）五元素只是前導，答案在六類作為

通道	立體人行系統、空橋、地面層退縮帶 本案 4 M 退縮帶＋跨渠橋
節點	立體轉運與停車節點 停車棟收納路徑停車亂象
地標	垂直量體成為方向感來源 攀岩牆為立體地標

（二）六類立體韌性作為

1. 立體交通：停車與轉運上樓下地，釋出地面給人。
2. 立體防洪：抬高避難層、獨立滯蓄槽、地下出入口反樓檐。
3. 立體綠化：立面綠化、屋頂多目標與綠屋頂降溫。
4. 立體能源：屋頂光電與遮蔭並置，減少熱得與能耗。
5. 立體避難：各層避難層與二方向逃生，屋頂為待援平台。
6. 立體混合：公益與營利垂直分層，一地多時段使用。

⚠ 停車場兼滯洪不得使有人或有車區域受淹；
本案改設獨立滯蓄槽並交代緊急斷電與復原管理。

（三）小結

立體化不是把樓蓋高，而是把「地面」這個最稀有的資源還給人。
本案把停車疊起來，換回廣場、市集與運動——韌性由此可見。

本年官方圖說要求｜逐項打勾

規劃理念與全區配置 ≥1/400 園道對策、出入口、停車場出入口、開挖、景觀、人車、防救災	✓
一樓平面 大廳、健康餐飲、停車出入口、等待區與退縮帶皆在圖上	✓
剖立面 A-A' 園道關係與控高／B-B' 運動淨高與天際線	✓
透視 ≥1 西側主視覺廣場望園道，含人物與親水平台	✓

數值證據分級（本張圖）
題目給定：80%／400%、運動需求坪數、退縮 4 M、12 M 道路、33 M 園道、14 M 渠
圖推概算：A＝50×54＋32×28＝3,596 ㎡（正文另稱約 3,600 ㎡）
自訂方案：分棟、棲層、停車約 155 輛、開挖範圍、封街與減速帶
題目未指定：汽車總數、機車以外之細部配比 → 圖上明寫未指定

交卷前：圖名・比例尺・指北・剖面標高數字、
透視有人物、每條算式數字與圖上一致、
題目點名條件逐條指得出位置。

法規檢核｜法源→本案落點

法源（簡稱）	要求	本案落點
多目標使用辦法	多目標容積一般 ≤ 總容積 1/3	4,400 ≤ 4,794.7 ㎡ ✓（餘裕 102.5）
同辦法附表	立體停車場高度「超過」6F/18M 之准許條件	題目要求原則「不超過」，兩者非同一上限
技則 §162-1-3	法定停車空間得不計入容積	停車棟樓地板不計入 F
技則 §59	停車空間依用途與樓地板核算	餐飲另涉至少標準二倍之停車檢核
技則 §302／§305	綠化量與基地保水	立面綠化＋退縮帶綠帶＋透水鋪面
技則 §4-3	雨水貯量：基地面積×0.045 m³/㎡	3,596×0.045 ≒ 161.8 m³
技則 §141	防空避難設備	B1 兼防空避難，出入口面街角廣場
都市設計基準	西、南側均退縮 4 M 無遮蓋帶	騎樓退到該帶之外，不覆蓋無遮蓋帶

※ 修號僅供本庫查核；考場圖上寫簡稱即可，不背條號。

課題→對策→效益（三行原則）

課題｜停車若最大化，地面與高度都會被吃掉
對策｜停車立體收納 6F／≤18 M，取最大值 7–8 成；省下的換成廣場、市集與運動
效益｜考官問「少掉的停車換成什麼」，圖上答得出來

課題｜與園道隔 12 M 道路，看得到走不到
對策｜設小橋／石階跨 14 M 排水渠，並重穿越與視線；道路仍完整保留
效益｜達成題目要求的「部分連接」，且不侵占對岸

課題｜六層不等於六個 3 M 樓層
對策｜運動另立 5F 棟；羽球淨高 6.1 M＋結構設備，剖面標明兩棟高度關係
效益｜控高的說法能被剖面驗證，而不是口號

課題｜停車場兼滯洪可能讓人與車受淹
對策｜改設獨立滯蓄槽，並交代緊急斷電、安全路徑與復原管理
效益｜防洪作為不製造新的人身風險

基地核對｜與官方底圖疊合

道路	西 12M／南 20M／北 7M；東緊臨街屋	✓ 未新增、未拓寬
園道	33 M，在 12 M 道路對側、基地外	✓ 未達成自家綠地，盡出穿越
排水渠	園道中央 14 M，水位低道路約 2 M	✓ 位置未移，以橋跨越
凹口	南段縮為 32 M 寬	✓ 保留退縮，未填平
退縮	西、南側「均」退 4 M 無遮蓋	✓ 兩側都畫，非僅西南角
開放面	西側整條面園道	✓ 量體退向東／中，西留 12 M 帶
界線	量體與開挖均在界內	✓ 東側留 3 M 防火間隔

量體計算式（逐行可校核）
A ＝ 50×54＋32×28 ＝ 2,700＋896 ＝ 3,596 ㎡〔圖示量取；正文約 3,600 ㎡，分母不混用〕
B上限 ＝ A×80% ＝ 2,876.8 ㎡　F上限 ＝ A×400% ＝ 14,384 ㎡
投影 B ＝ 停車棟 891＋運動棟 880 ＝ 1,771 ㎡　建蔽 ＝ 49.2% ≦ 60%（自訂）≦ 80% ✓
運動需求 ＝ (300＋200＋500＋300) 坪 × 400/121 ≒ 4,297.5 ㎡〔題目給定下限〕
多目標容積門檻 ＝ 14,384 × 1/3 ＝ 4,794.7 ㎡
運動棟 F ＝ 880 × 5F ＝ 4,400 ㎡　→ 4,297.5 ≦ 4,400 ≦ 4,794.7 ✓（餘裕 102.5 ㎡）
停車 ＝ (891×6F＋B1 891)＋40 ≒ 155 輛〔方案・刻意不衝滿，換取西側帶狀開放空間〕
開挖 D ＝ 35M × 47M ＝ 1,645 ㎡　開挖率 ＝ 45.7%〔題目點名須標〕
雨水貯集 ＝ 3,596 × 0.045 ≒ 161.8 m³（技則 §4-3）